



ในแผ่นผนังแต่ละแนว

- 1. ผนังขยาย: A อยู่ซ้าย และ B อยู่ขวา
- 2. P00, P01... = จุดแบ่งตามแนวแกนผนัง
- 3. ระยะย่อ = จากจุดก่อนหน้าไปจุดปัจจุบัน
- 4. ระยะสะสม = จาก A ถึงจุดนั้น
- 5. รูปด้านคือแสดงความสูงช่องเปิดจริงในไฟล์

รหัสเหตุการณ์ในตารางจุด

A / B	ต้น / ปลายแกนผนัง
DxxL / DxxR	ขอบประตูแรก / ท้าย ตาม A→B
WxxL / WxxR	ขอบหน้าต่างแรก / ท้าย ตาม A→B
Jxx	จุดตัดแกนกับผนัง WLxx
Jxx- / Jxx+	ผิวผนังที่ตัดแกน ก่อน / หลังจุดตัด
Cxx / Pxx	ศูนย์กลางเสาตามรหัสโมเดล
Cxx- / Cxx+	ขอบเสาที่ฉายตามแกน ก่อน / หลัง

ขอบเขตของระยะ

เส้นระยะย่อแบ่งแกนที่ทุกจุดอ้างอิง
บางช่วงอยู่ในเนื้อผนังหรือเสา ไม่ใช่ช่องว่าง
ผิวผนัง = แกน ± ครึ่งความหนาในไฟล์
ยังไม่รวมจาบหรือวัสดุกรุที่ไม่ระบุในแบบ
รูปด้านคืออ่านจาก A→B ไม่ขึ้นกับทิศบานเปิด
จุดที่เกิน A-B แสดงแยก ไม่ใช้รวมความยาว

D09 เกินปลาย WL17 อยู่ 0.010 ม.

หน้าผนัง: 1:25 หรือ 1:50 ตามที่ระบุ

รูปด้าน: 1:50 • พิมพ์ A3 / 100%

ปีระยะ 0.001 ม. จุดที่ปิดได้ค่าเดียวกันรวมแถว


OHM HOUSE

WL01 / ระยะย่อทุกจุด


ผังขยาย 1:50 • รูปด้านคลี่ 1:50 • ระยะทั้งหมดเป็นเมตร • ยาว 11.000 / สูง 3.000 / หน้า 0.120

A (0.000, 0.000) → B (11.000, 0.000) ในแกน (X,Z)

ผังขยายตามแกน A→B / 1:50

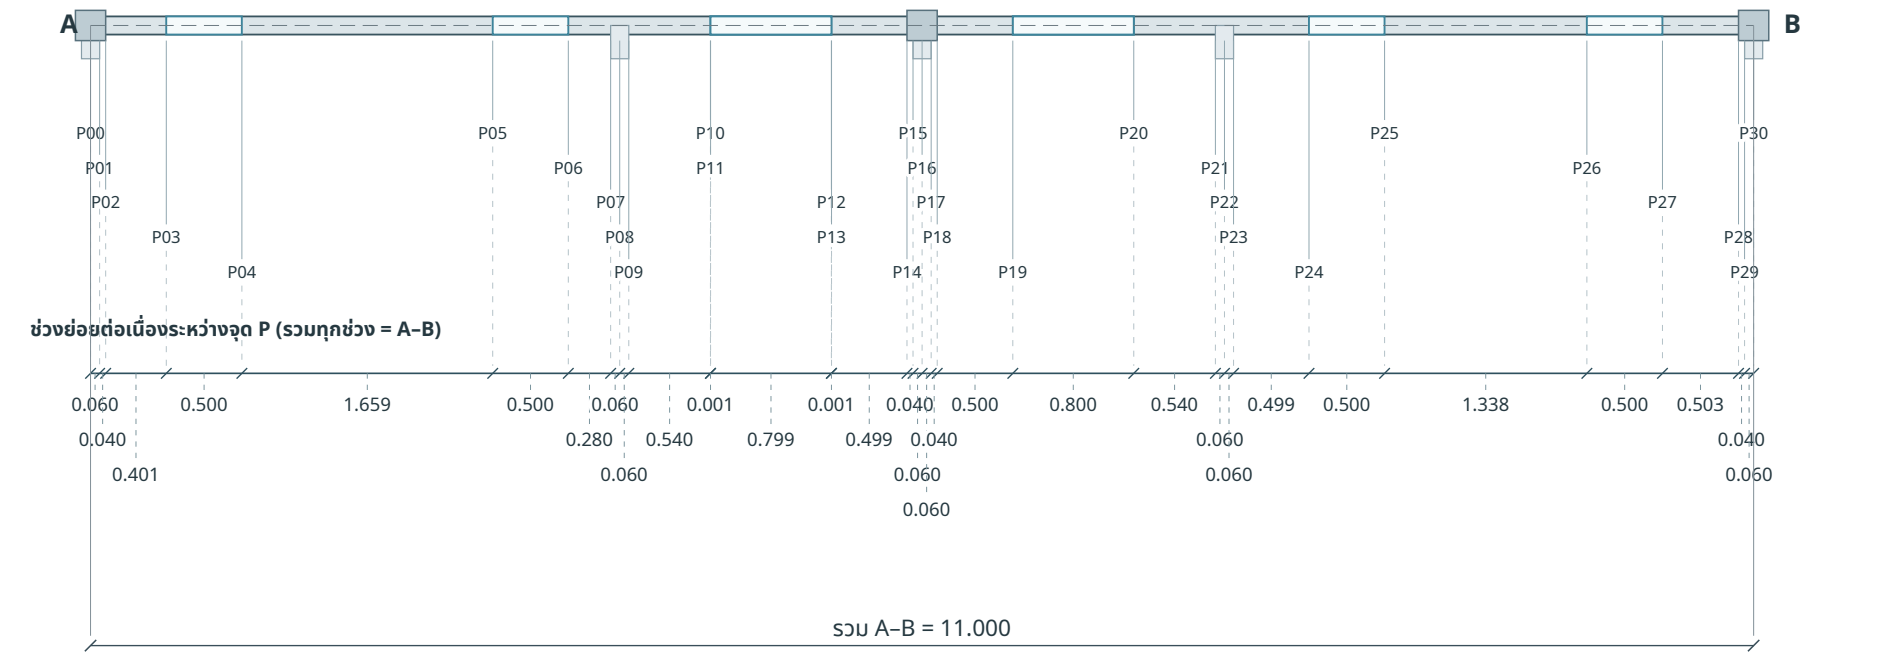

รูปด้านคลี่ A→B / 1:50

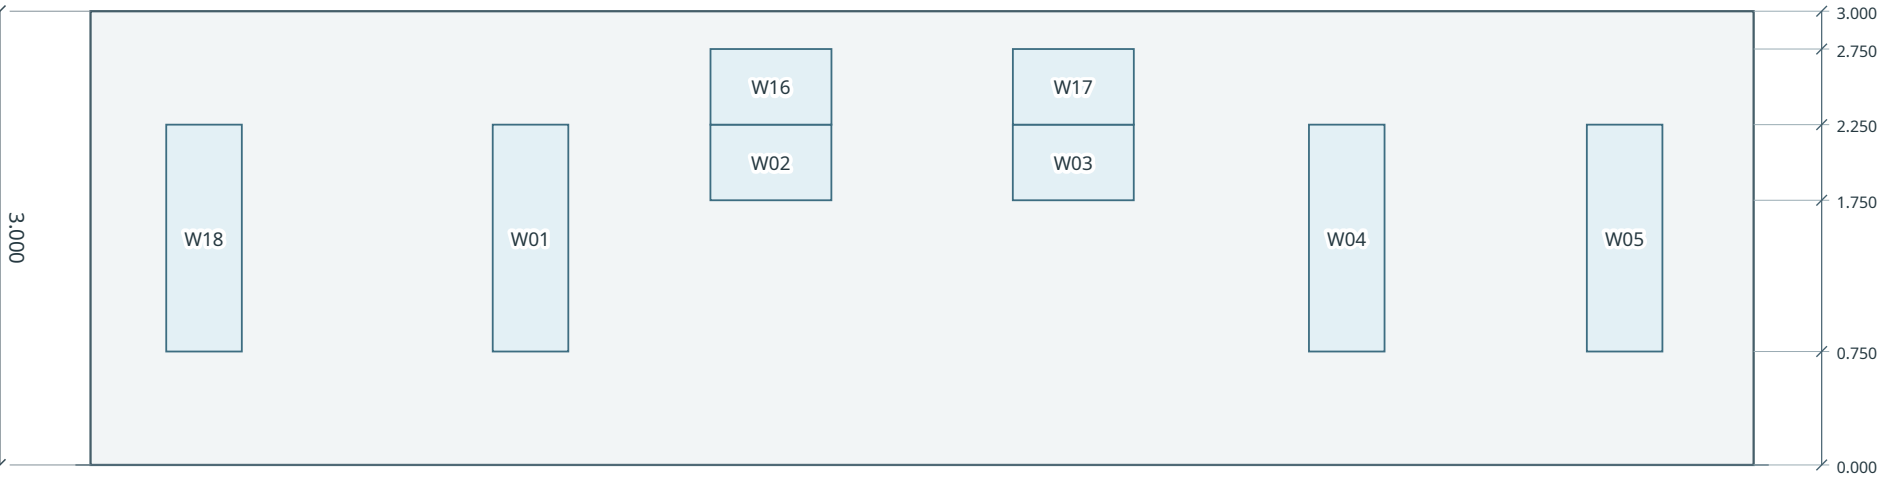

ช่องเปิด: กว้าง×สูง | A→ขอบแรก / ขอบท้าย→B | ขอบล่าง / หัวช่อง

W01 0.500×1.500 2.660/7.840 0.750/2.250	W02 0.800×0.500 4.100/6.100 1.750/2.250
W03 0.800×0.500 6.100/4.100 1.750/2.250	W04 0.500×1.500 8.059/2.441 0.750/2.250
W05 0.500×1.500 9.897/0.603 0.750/2.250	W16 0.800×0.500 4.101/6.099 2.250/2.750
W17 0.800×0.500 6.100/4.100 2.250/2.750	W18 0.500×1.500 0.501/9.999 0.750/2.250

จุด	จาก A	ช่วงย่อย	ตำแหน่ง / เหตุการณ์
P00	0.000	—	A / J09 / C1
P01	0.060	0.060	J09+
P02	0.100	0.040	C1+
P03	0.501	0.401	W18L
P04	1.001	0.500	W18R
P05	2.660	1.659	W01L
P06	3.160	0.500	W01R
P07	3.440	0.280	J10-
P08	3.500	0.060	J10
P09	3.560	0.060	J10+
P10	4.100	0.540	W02L
P11	4.101	0.001	W16L
P12	4.900	0.799	W02R
P13	4.901	0.001	W16R
P14	5.400	0.499	C2-
P15	5.440	0.040	J13-
P16	5.500	0.060	J13 / C2
P17	5.560	0.060	J13+
P18	5.600	0.040	C2+
P19	6.100	0.500	W03L / W17L
P20	6.900	0.800	W03R / W17R
P21	7.440	0.540	J17-
P22	7.500	0.060	J17
P23	7.560	0.060	J17+
P24	8.059	0.499	W04L
P25	8.559	0.500	W04R
P26	9.897	1.338	W05L
P27	10.397	0.500	W05R
P28	10.900	0.503	C3-
P29	10.940	0.040	J02-
P30	11.000	0.060	B / J02 / C3

รวมช่วงย่อย 11.000 ม.

ตำแหน่งจาก A ที่อยู่นอก A-B (ไม่นับรวม)

C1- -0.100 ม.	J09- -0.060 ม.
J02+ 11.060 ม.	C3+ 11.100 ม.


OHM HOUSE

WL02 / ระยะย่อทุกจุด


ผังขยาย 1:25 • รูปด้านคลี่ 1:50 • ระยะทั้งหมดเป็นเมตร • ยาว 5.000 / สูง 3.000 / หน้า 0.120

A (11.000, 0.000) → B (11.000, 5.000) ในแกน (X,Z)

ผังขยายตามแกน A→B / 1:25

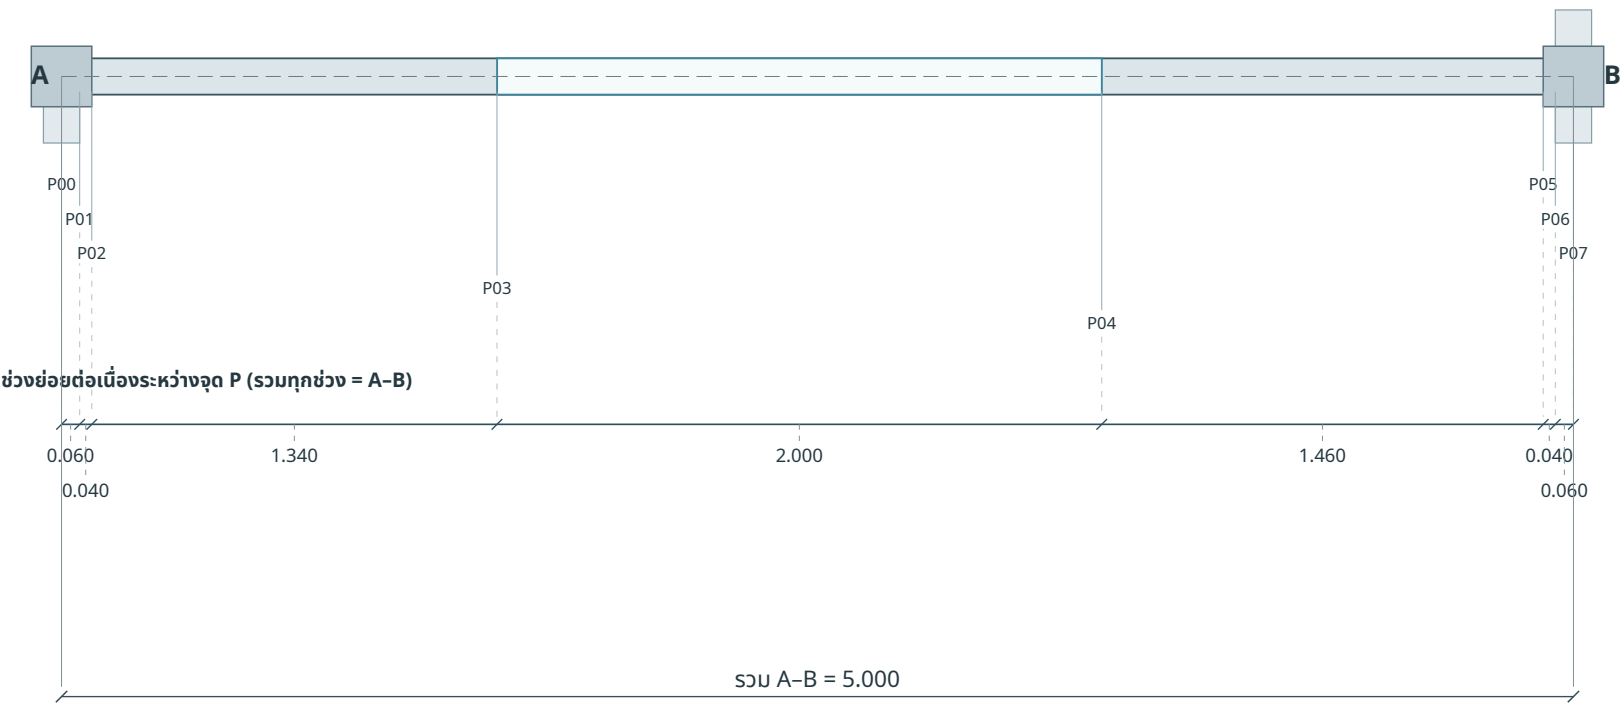

รูปด้านคลี่ A→B / 1:50

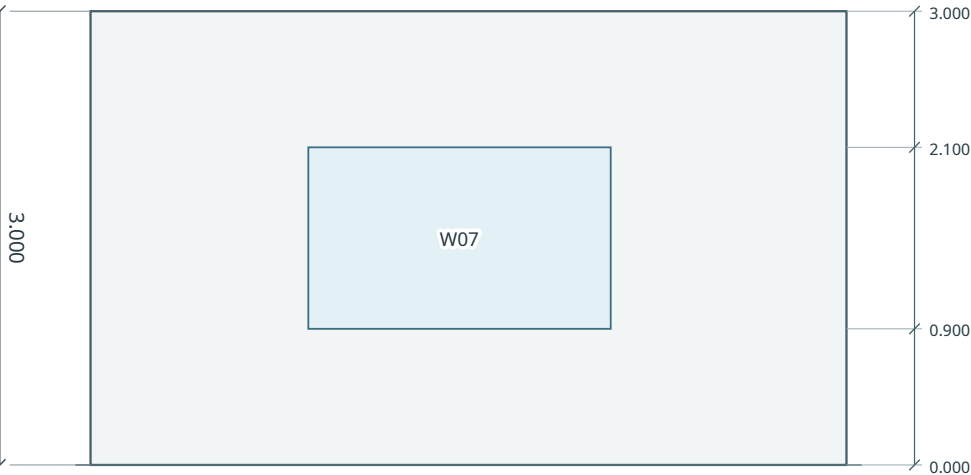

ช่องเปิด: กว้าง×สูง | A→ขอบแรก / ขอบท้าย→B | ขอบล่าง / หัวช่อง

W07 2.000×1.200 | 1.440/1.560 | 0.900/2.100

ชุดแปลนประกอบการวางแผน • อ้างอิง Pascal V384 / ข้อมูล 11 ก.ย. 2026

หน่วย: เมตร | พิมพ์ Actual size / 100% • ห้ามเลือก Fit to page

ระยะตามไฟล์แบบ ไม่ใช่ระยะสุกหลิงจาบ • ตรวจสอบงานก่อนก่อสร้างหรือสั่งผลิต

ตรวจขนาดพิมพ์: เส้นนี้ต้องยาว 100 มม.

สร้างชุดเอกสาร 4 ต.ค. 2026

WD-03 / 22

A3 • 420 × 297 มม.


OHM HOUSE

WL03 / ระยะย่อทุกจุด


ผังขยาย 1:25 • รูปด้านคลี่ 1:50 • ระยะทั้งหมดเป็นเมตร • ยาว 1.790 / สูง 3.000 / หน้า 0.120

A (11.000, 5.000) → B (12.790, 5.000) ในแกน (X,Z)

ผังขยายตามแกน A→B / 1:25

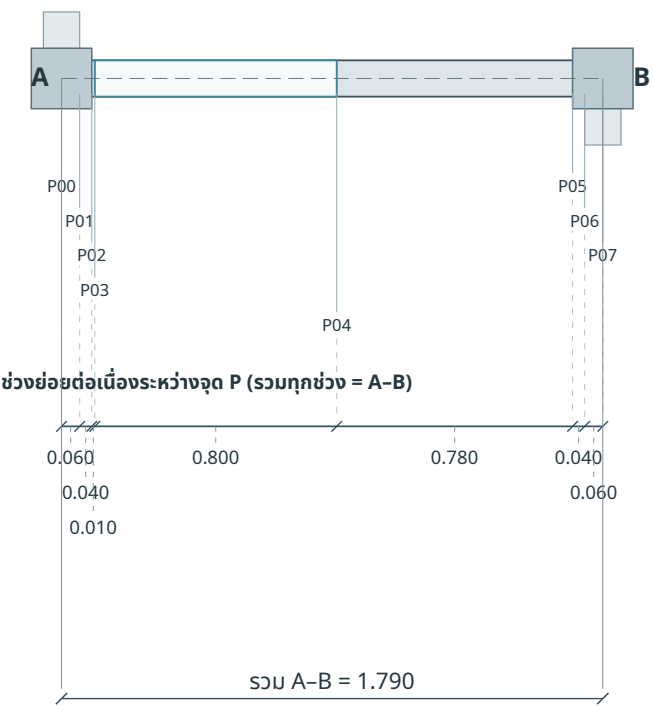

รูปด้านคลี่ A→B / 1:50

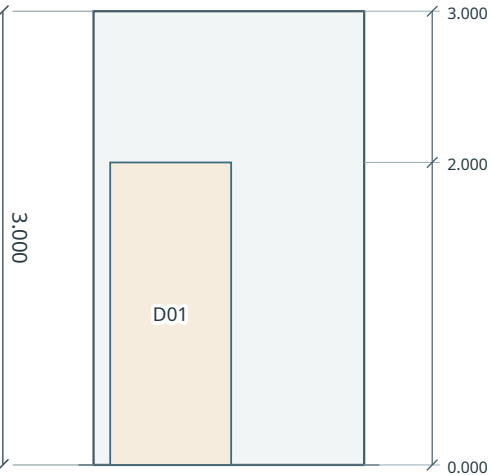

ช่องเปิด: กว้าง×สูง | A→ขอบแรก / ขอบท้าย→B | ขอบล่าง / หัวช่อง

D01 0.800×2.000 | 0.110/0.880 | 0.000/2.000

จุด	จาก A	ช่วงย่อ	ตำแหน่ง / เหตุการณ์
P00	0.000	—	A / J02 / J19 / C9
P01	0.060	0.060	J02+
P02	0.100	0.040	C9+
P03	0.110	0.010	D01L
P04	0.910	0.800	D01R
P05	1.690	0.780	C10-
P06	1.730	0.040	J04-
P07	1.790	0.060	B / J04 / C10

รวมช่วงย่อ 1.790 ม.

ตำแหน่งจาก A ที่อยู่นอก A-B (ไม่นับรวม)

C9- -0.100 ม. J02- -0.060 ม.
J04+ 1.850 ม. C10+ 1.890 ม.


OHM HOUSE

WL04 / ระยะย่อทุกจุด


ผังขยาย 1:25 • รูปด้านคลี่ 1:50 • ระยะทั้งหมดเป็นเมตร • ยาว 4.380 / สูง 3.000 / หน้า 0.120

A (12.790, 5.000) → B (12.790, 9.380) ในแกน (X,Z)

ผังขยายตามแกน A→B / 1:25

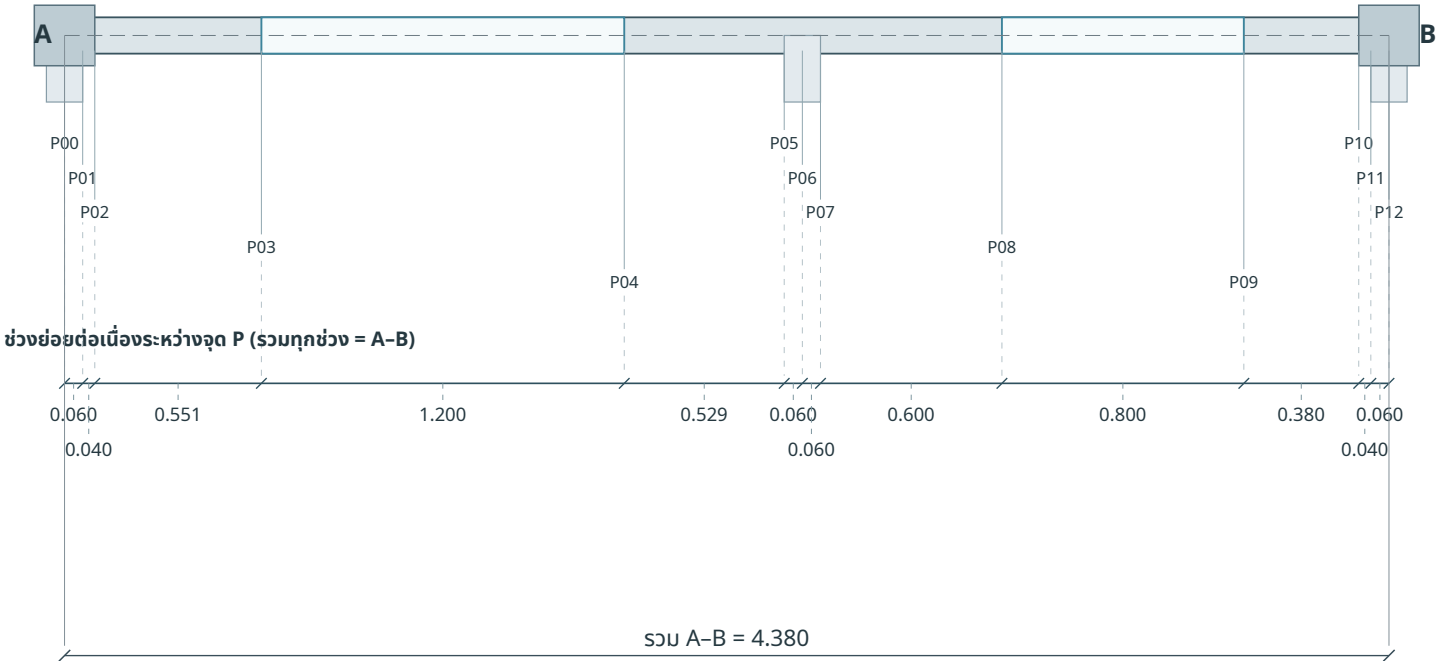

รูปด้านคลี่ A→B / 1:50

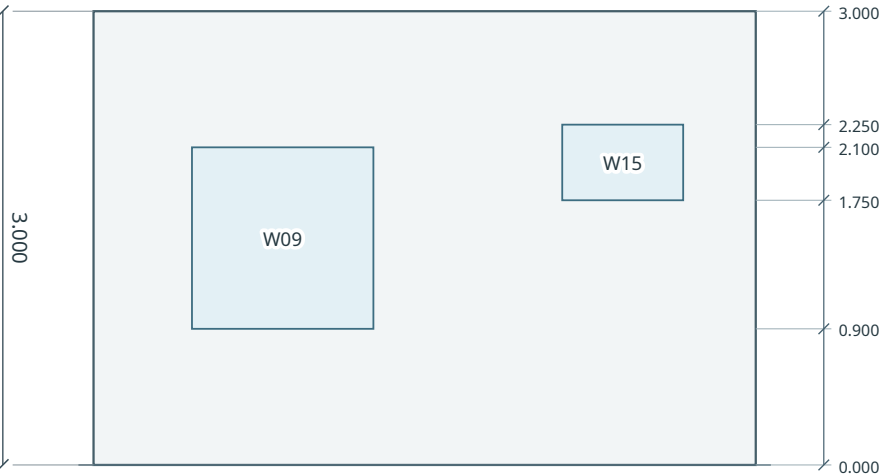

จุด	จาก A	ช่วงย่อย	ตำแหน่ง / เหตุการณ์
P00	0.000	—	A / J03 / C10
P01	0.060	0.060	J03+
P02	0.100	0.040	C10+
P03	0.651	0.551	W09L
P04	1.851	1.200	W09R
P05	2.380	0.529	J20-
P06	2.440	0.060	J20
P07	2.500	0.060	J20+
P08	3.100	0.600	W15L
P09	3.900	0.800	W15R
P10	4.280	0.380	C12-
P11	4.320	0.040	J05-
P12	4.380	0.060	B / J05 / C12

รวมช่วงย่อย 4.380 ม.

ตำแหน่งจาก A ที่อยู่นอก A-B (ไม่นับรวม)

C10- -0.100 ม. J03- -0.060 ม.
J05+ 4.440 ม. C12+ 4.480 ม.

WL05 / រະមះម៉່យកុកតុត

A (12.790, 9.380) $\rightarrow$ B (11.000, 9.380) ໄບແຄນ (X,Z)

Diagram illustrating the vertical alignment of the window (W13) within the room height. The room height is 3.000m. The window height is 1.550m. The distance from the window top to the ceiling is 2.050m.

W13 0.800×0.500 | 0.495/0.495 | 1.550/2.050

จุด	จาก A	ช่วงย่อย	ตำแหน่ง / เหตุการณ์
P00	0.000	—	A / J04 / C12
P01	0.060	0.060	J04+
P02	0.100	0.040	C12+
P03	0.495	0.395	W13L
P04	1.295	0.800	W13R
P05	1.690	0.395	C11-
P06	1.730	0.040	J06- / J21-
P07	1.790	0.060	B / J06 / J21 / C11

ตำแหน่งจาก A ที่อยู่นอก A-B (ไม่นับรวม)

C12- -0.100 u.	J04- -0.060 u.
J06+ 1.850 u.	J21+ 1.850 u.
C11+ 1.890 u.	


OHM HOUSE

WL06 / ระยะย่อทุกจุด


ผังขยาย 1:25 • รูปด้านคลี่ 1:50 • ระยะทั้งหมดเป็นเมตร • ยาว 3.500 / สูง 3.000 / หน้า 0.120

A (11.000, 9.380) → B (11.000, 12.880) ในแกน (X,Z)

ผังขยายตามแกน A→B / 1:25

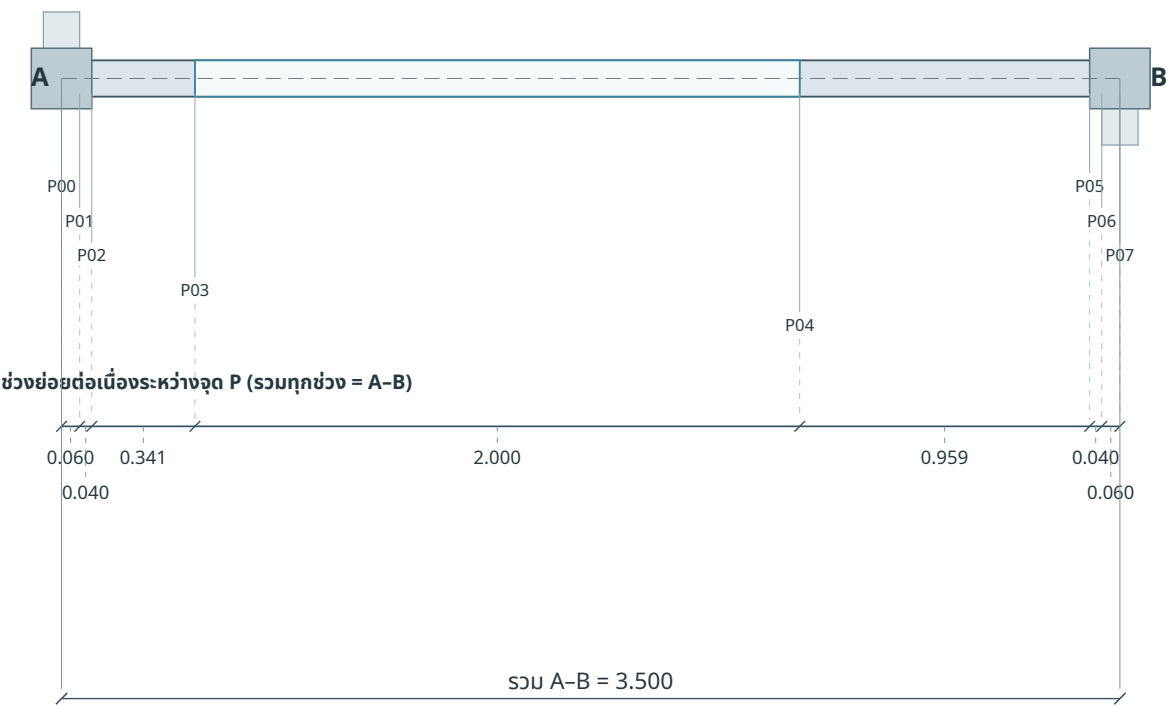

รูปด้านคลี่ A→B / 1:50

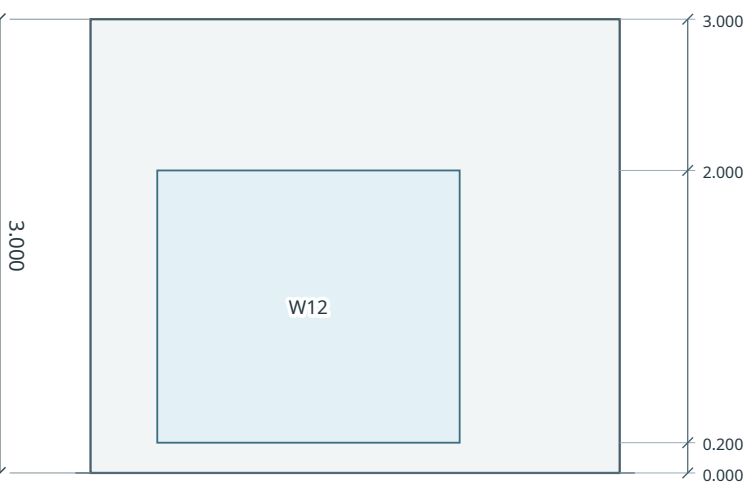

จุด	จาก A	ช่วงย่อ	ตำแหน่ง / เหตุการณ์
P00	0.000	—	A / J05 / J21 / C11
P01	0.060	0.060	J05+
P02	0.100	0.040	C11+
P03	0.441	0.341	W12L
P04	2.441	2.000	W12R
P05	3.400	0.959	C14-
P06	3.440	0.040	J07-
P07	3.500	0.060	B / J07 / C14

รวมช่วงย่อ 3.500 ม.

ตำแหน่งจาก A ที่อยู่นอก A-B (ไม่นับรวม)

C11- -0.100 ม.	J05- -0.060 ม.
J07+ 3.560 ม.	C14+ 3.600 ม.


OHM HOUSE

WL07 / ระยะย่อทุกจุด


ผังขยาย 1:25 • รูปด้านคลี่ 1:50 • ระยะทั้งหมดเป็นเมตร • ยาว 5.500 / สูง 3.000 / หน้า 0.120

A (11.000, 12.880) → B (5.500, 12.880) ในแกน (X,Z)

ผังขยายตามแกน A→B / 1:25

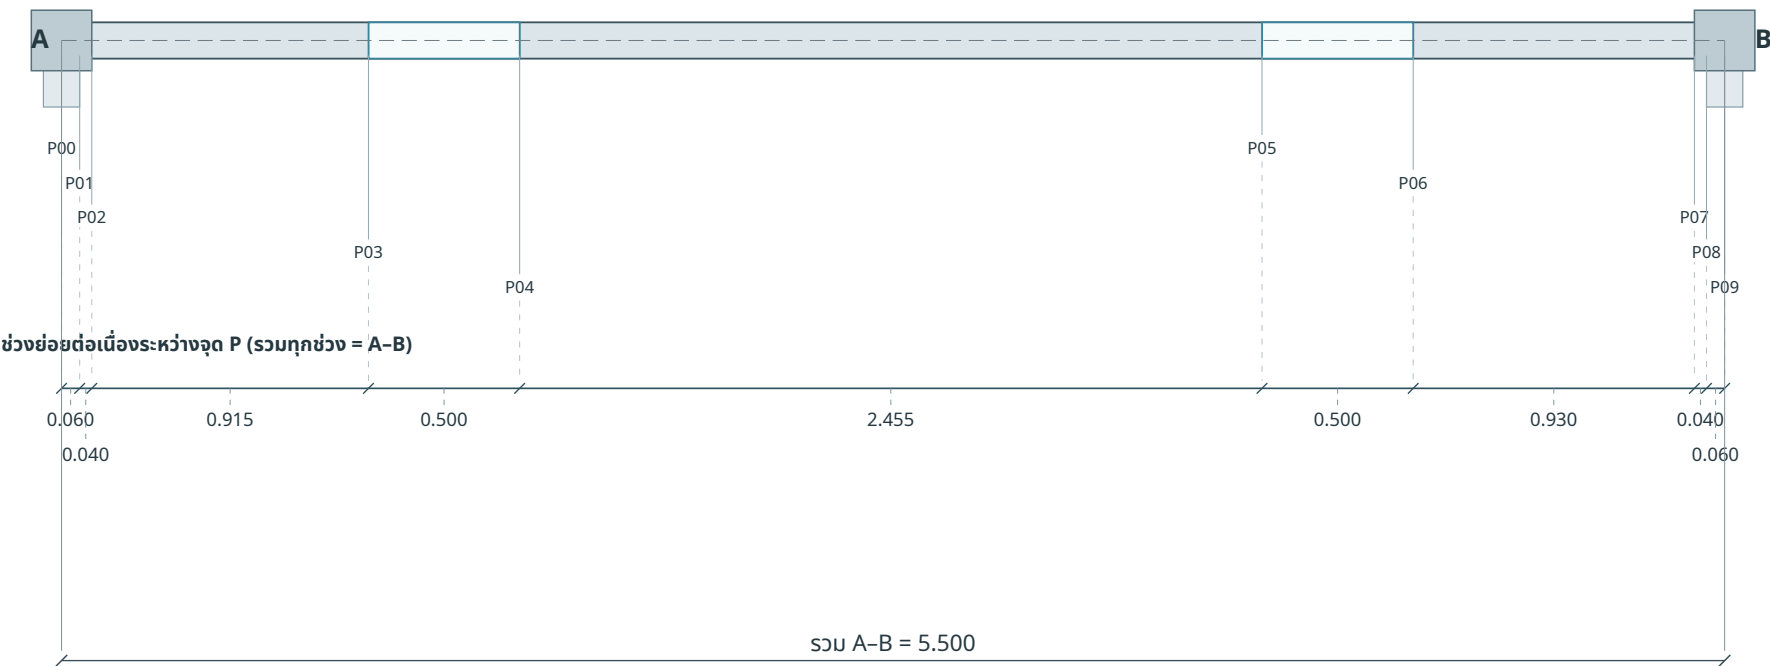

รูปด้านคลี่ A→B / 1:50

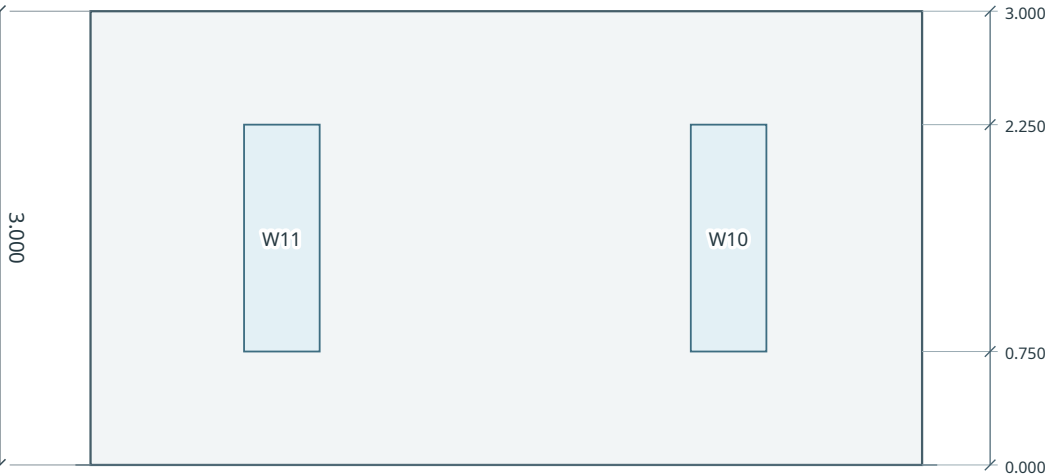

ช่องเปิด: กว้าง×สูง | A→ขอบแรก / ขอบท้าย→B | ขอบล่าง / หัวช่อง

W10 0.500×1.500 | 3.970/1.030 | 0.750/2.250

W11 0.500×1.500 | 1.015/3.985 | 0.750/2.250

จุด	จาก A	ช่วงย่อย	ตำแหน่ง / เหตุการณ์
P00	0.000	—	A / J06 / C14
P01	0.060	0.060	J06+
P02	0.100	0.040	C14+
P03	1.015	0.915	W11L
P04	1.515	0.500	W11R
P05	3.970	2.455	W10L
P06	4.470	0.500	W10R
P07	5.400	0.930	C13-
P08	5.440	0.040	J15-
P09	5.500	0.060	B / J15 / C13

รวมช่วงย่อย 5.500 ม.

ตำแหน่งจาก A ที่อยู่นอก A-B (ไม่นับรวม)

C14- -0.100 ม.

J06- -0.060 ม.

J15+ 5.560 ม.

C13+ 5.600 ม.


OHM HOUSE

WL08 / ระยะย่อทุกจุด


ผังขยาย 1:25 • รูปด้านคลี่ 1:50 • ระยะทั้งหมดเป็นเมตร • ยาว 2.500 / สูง 3.000 / หน้า 0.120

A (2.500, 5.000) → B (0.000, 5.000) ในแกน (X,Z)

ผังขยายตามแกน A→B / 1:25

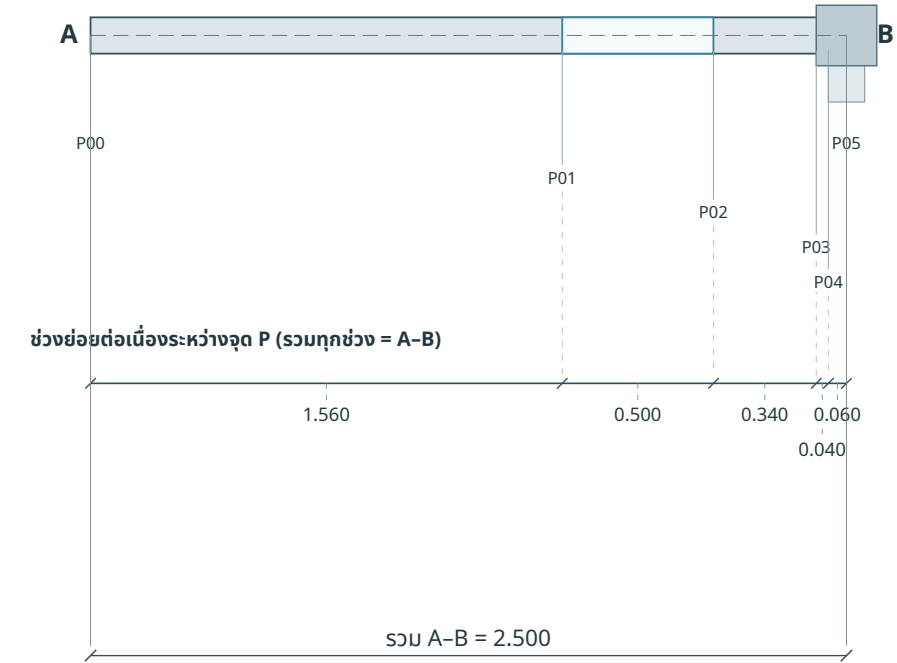

รูปด้านคลี่ A→B / 1:50

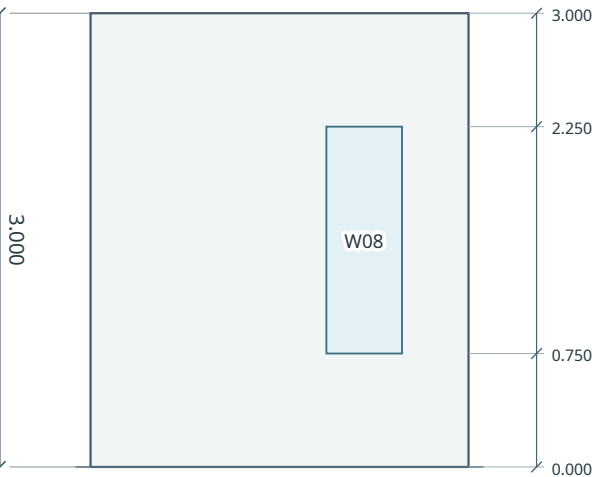

ช่องเปิด: กว้าง×สูง | A→ขอบแรก / ขอบท้าย→B | ขอบล่าง / หัวช่อง

W08 0.500×1.500 | 1.560/0.440 | 0.750/2.250

จุด	จาก A	ช่วงย่อย	ตำแหน่ง / เหตุการณ์
P00	0.000	—	A / J16
P01	1.560	1.560	W08L
P02	2.060	0.500	W08R
P03	2.400	0.340	C6-
P04	2.440	0.040	J09-
P05	2.500	0.060	B / J09 / C6

รวมช่วงย่อย 2.500 ม.

ตำแหน่งจาก A ที่อยู่นอก A-B (ไม่นับรวม)

J09+ 2.560 ม.

C6+ 2.600 ม.


OHM HOUSE

WL09 / ระยะย่อทุกจุด


ผังขยาย 1:25 • รูปด้านคลี่ 1:50 • ระยะทั้งหมดเป็นเมตร • ยาว 5.000 / สูง 3.000 / หน้า 0.120

A (0.000, 5.000) → B (0.000, 0.000) ในแกน (X,Z)

ผังขยายตามแกน A→B / 1:25

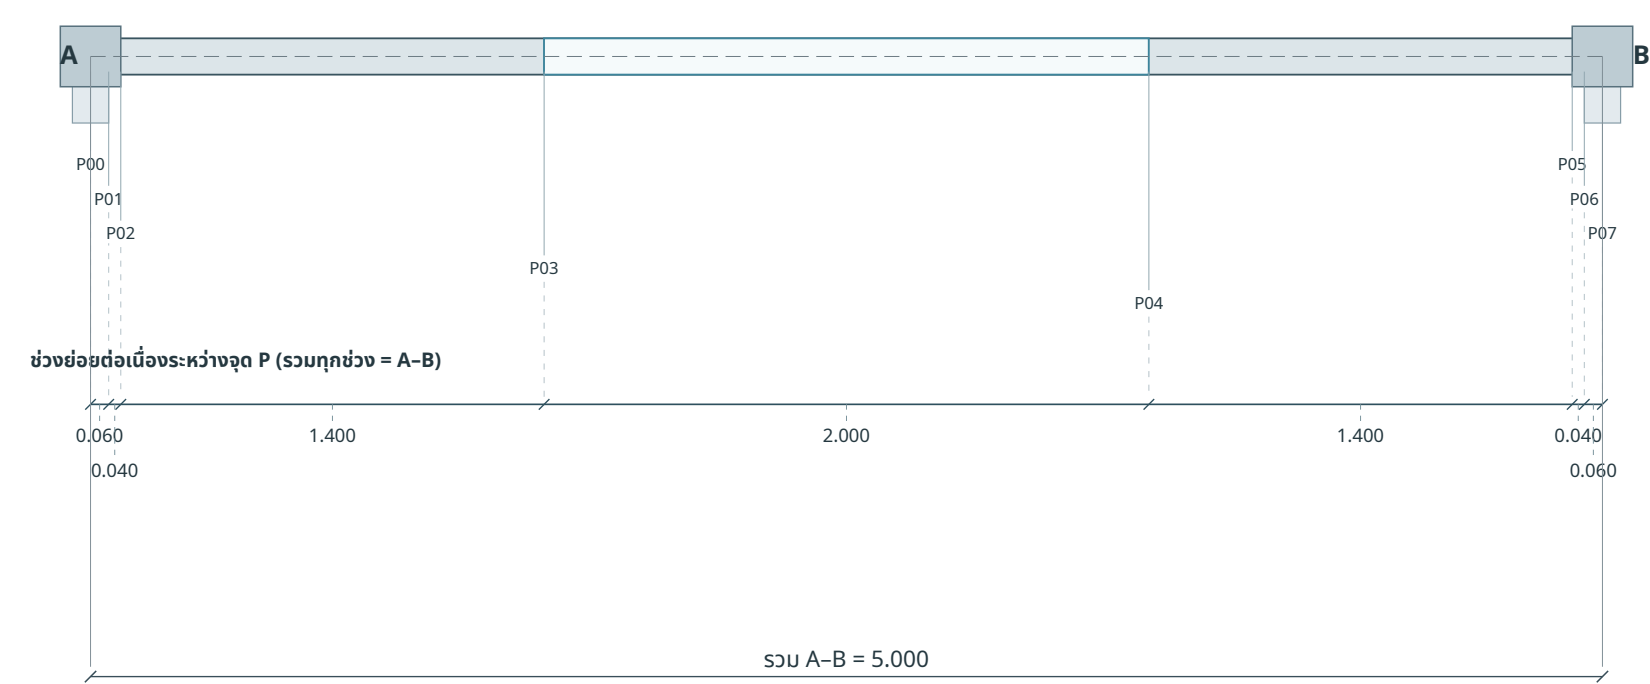

รูปด้านคลี่ A→B / 1:50

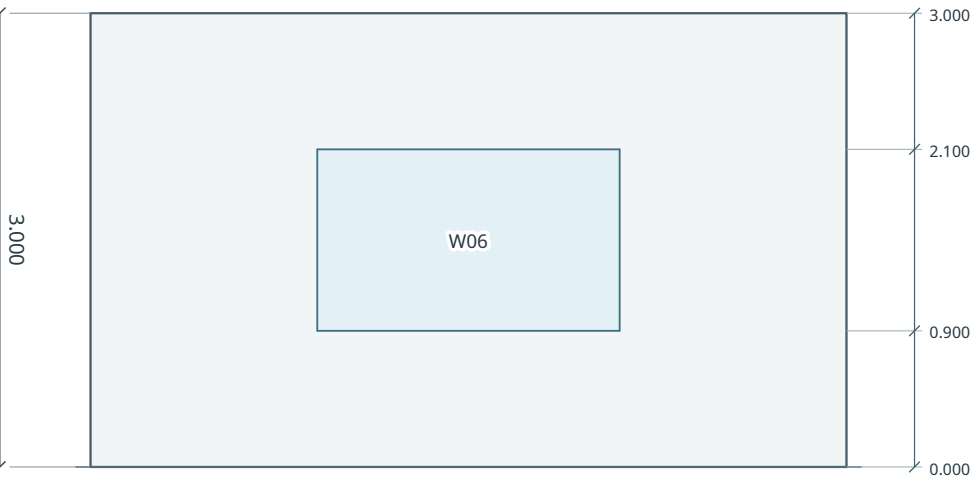

ช่องเปิด: กว้าง×สูง | A→ขอบแรก / ขอบท้าย→B | ขอบล่าง / หัวช่อง

W06 2.000×1.200 | 1.500/1.500 | 0.900/2.100

จุด	จาก A	ช่วงย่อย	ตำแหน่ง / เหตุการณ์
P00	0.000	—	A / J08 / C6
P01	0.060	0.060	J08+
P02	0.100	0.040	C6+
P03	1.500	1.400	W06L
P04	3.500	2.000	W06R
P05	4.900	1.400	C1-
P06	4.940	0.040	J01-
P07	5.000	0.060	B / J01 / C1

รวมช่วงย่อย 5.000 ม.

ตำแหน่งจาก A ที่อยู่นอก A-B (ไม่นับรวม)

C6- -0.100 ม. J08- -0.060 ม.
J01+ 5.060 ม. C1+ 5.100 ม.


OHM HOUSE

WL10 / ระยะย่อทุกจุด


ผังขยาย 1:25 • รูปด้านคลี่ 1:50 • ระยะทั้งหมดเป็นเมตร • ยาว 2.940 / สูง 3.000 / หน้า 0.120

A (3.500, 0.000) → B (3.500, 2.940) ในแกน (X,Z)

ผังขยายตามแกน A→B / 1:25

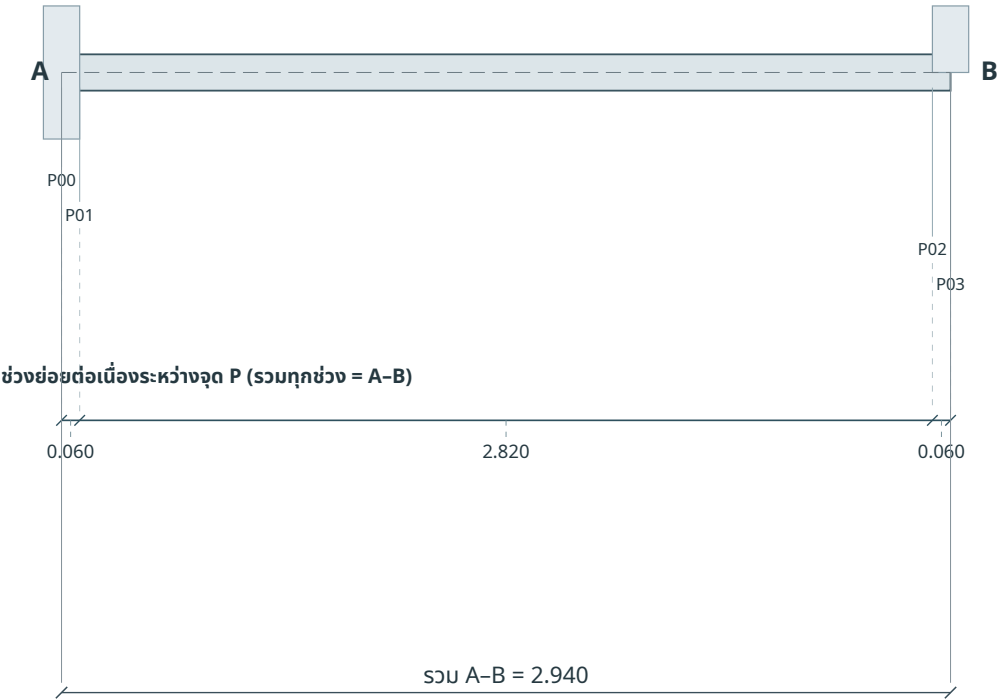

รูปด้านคลี่ A→B / 1:50

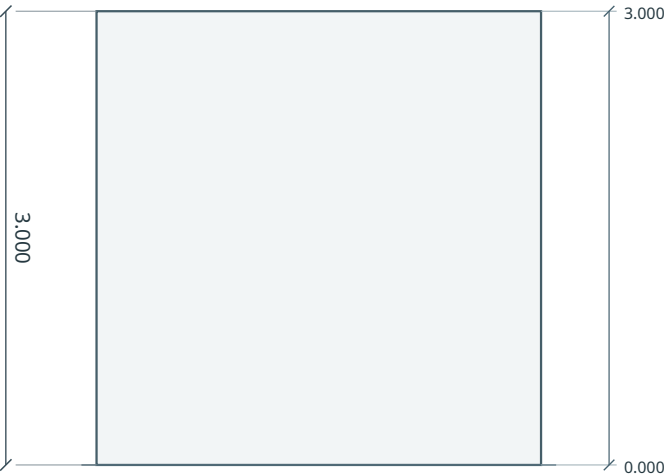

ช่องเปิด: กว้าง×สูง | A→ขอบแรก / ขอบท้าย→B | ขอบล่าง / หัวช่อง

ไม่มีช่องเปิดในผนังแบบนี้ตามไฟล์

จุด	จาก A	ช่วงย่อ	ตำแหน่ง / เหตุการณ์
P00	0.000	—	A / J01
P01	0.060	0.060	J01+
P02	2.880	2.820	J11-
P03	2.940	0.060	B / J11

รวมช่วงย่อ 2.940 ม.

ตำแหน่งจาก A ที่อยู่นอก A-B (ไม่นับรวม)

J01 - -0.060 ม.

J11 + 3.000 ม.


OHM HOUSE

WL11 / ระยะย่อทุกจุด


ผังขยาย 1:25 • รูปด้านคลี่ 1:50 • ระยะทั้งหมดเป็นเมตร • ยาว 2.000 / สูง 3.000 / หน้า 0.120

A (3.500, 2.940) → B (5.500, 2.940) ในแกน (X,Z)

ผังขยายตามแกน A→B / 1:25

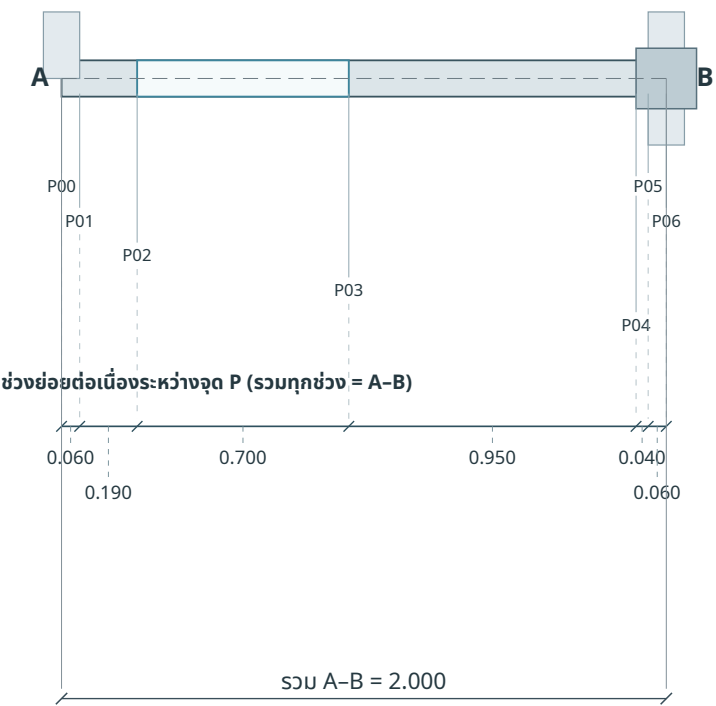

รูปด้านคลี่ A→B / 1:50

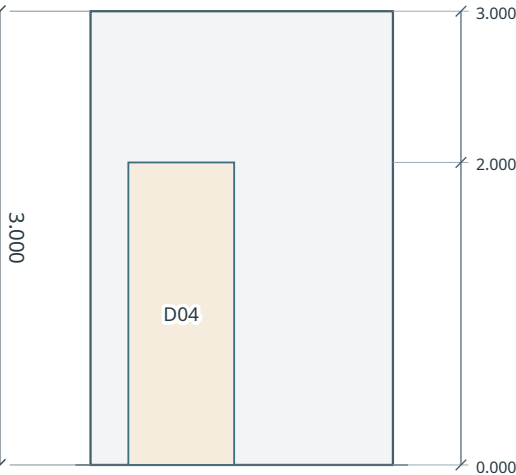

ช่องเปิด: กว้าง×สูง | A→ขอบแรก / ขอบท้าย→B | ขอบล่าง / หัวช่อง

D04 0.700×2.000 | 0.250/1.050 | 0.000/2.000

จุด	จาก A	ช่วงย่อย	ตำแหน่ง / เหตุการณ์
P00	0.000	—	A / J10
P01	0.060	0.060	J10+
P02	0.250	0.190	D04L
P03	0.950	0.700	D04R
P04	1.900	0.950	C4-
P05	1.940	0.040	J13- / J14-
P06	2.000	0.060	B / J12 / J13 / J14 / C4

รวมช่วงย่อย 2.000 ม.

ตำแหน่งจาก A ที่อยู่นอก A-B (ไม่นับรวม)

J10- -0.060 ม. J13+ 2.060 ม.
J14+ 2.060 ม. C4+ 2.100 ม.


OHM HOUSE

WL12 / ระยะย่อทุกจุด


ผังขยาย 1:25 • รูปด้านคลี่ 1:50 • ระยะทั้งหมดเป็นเมตร • ยาว 2.000 / สูง 3.000 / หน้า 0.120

A (5.500, 2.940) → B (7.500, 2.940) ในแกน (X,Z)

ผังขยายตามแกน A→B / 1:25

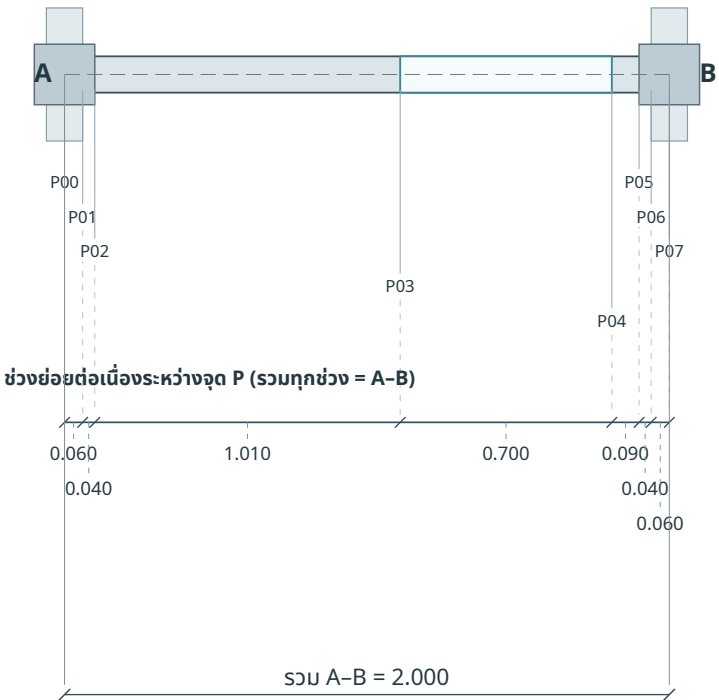

รูปด้านคลี่ A→B / 1:50

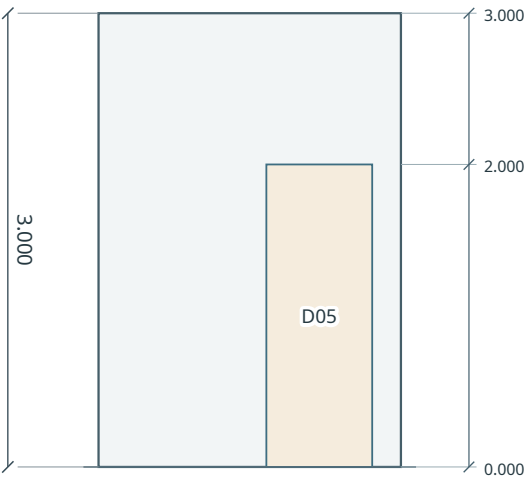

ช่องเปิด: กว้าง×สูง | A→ขอบแรก / ขอบท้าย→B | ขอบล่าง / หัวช่อง

D05 0.700×2.000 | 1.110/0.190 | 0.000/2.000

จุด	จาก A	ช่วงย่อย	ตำแหน่ง / เหตุการณ์
P00	0.000	—	A / J11 / J13 / J14 / C4
P01	0.060	0.060	J13+ / J14+
P02	0.100	0.040	C4+
P03	1.110	1.010	D05L
P04	1.810	0.700	D05R
P05	1.900	0.090	C5-
P06	1.940	0.040	J17- / J18-
P07	2.000	0.060	B / J17 / J18 / C5

รวมช่วงย่อย 2.000 ม.

ตำแหน่งจาก A ที่อยู่นอก A-B (ไม่นับรวม)

C4- -0.100 ม.	J13- -0.060 ม.
J14- -0.060 ม.	J17+ 2.060 ม.
J18+ 2.060 ม.	C5+ 2.100 ม.


OHM HOUSE

WL13 / ระยะย่อทุกจุด


ผังขยาย 1:25 • รูปด้านคลี่ 1:50 • ระยะทั้งหมดเป็นเมตร • ยาว 2.940 / สูง 3.000 / หน้า 0.120

A (5.500, 0.000) → B (5.500, 2.940) ในแกน (X,Z)

ผังขยายตามแกน A→B / 1:25

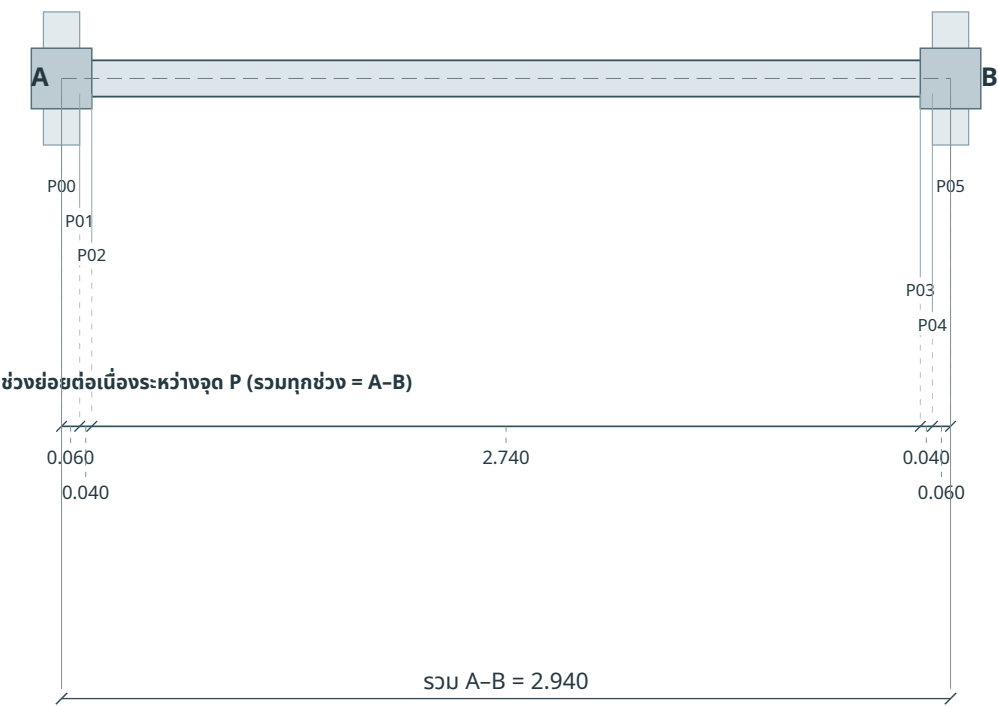

รูปด้านคลี่ A→B / 1:50

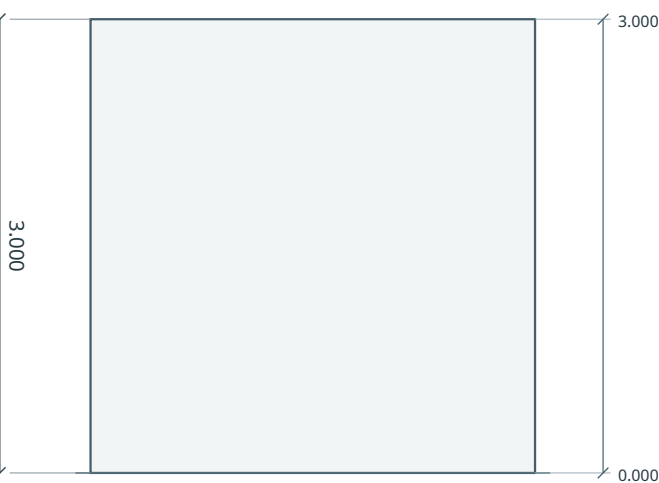

ช่องเปิด: กว้าง×สูง | A→ขอบแรก / ขอบท้าย→B | ขอบล่าง / หัวช่อง

ไม่มีช่องเปิดในผนังแนวนอนนี้ตามไฟล์

จุด	จาก A	ช่วงย่อ	ตำแหน่ง / เหตุการณ์
P00	0.000	—	A / J01 / C2
P01	0.060	0.060	J01+
P02	0.100	0.040	C2+
P03	2.840	2.740	C4-
P04	2.880	0.040	J11- / J12-
P05	2.940	0.060	B / J11 / J12 / J14 / C4

รวมช่วงย่อ 2.940 ม.

ตำแหน่งจาก A ที่อยู่นอก A-B (ไม่นับรวม)

C2- -0.100 ม. J01- -0.060 ม.

J11+ 3.000 ม. J12+ 3.000 ม.

C4+ 3.040 ม.


OHM HOUSE

WL14 / ระยะย่อทุกจุด


ผังขยาย 1:25 • รูปด้านคลี่ 1:50 • ระยะทั้งหมดเป็นเมตร • ยาว 2.060 / สูง 3.000 / หน้า 0.120

A (5.500, 2.940) → B (5.500, 5.000) ในแกน (X,Z)

ผังขยายตามแกน A→B / 1:25

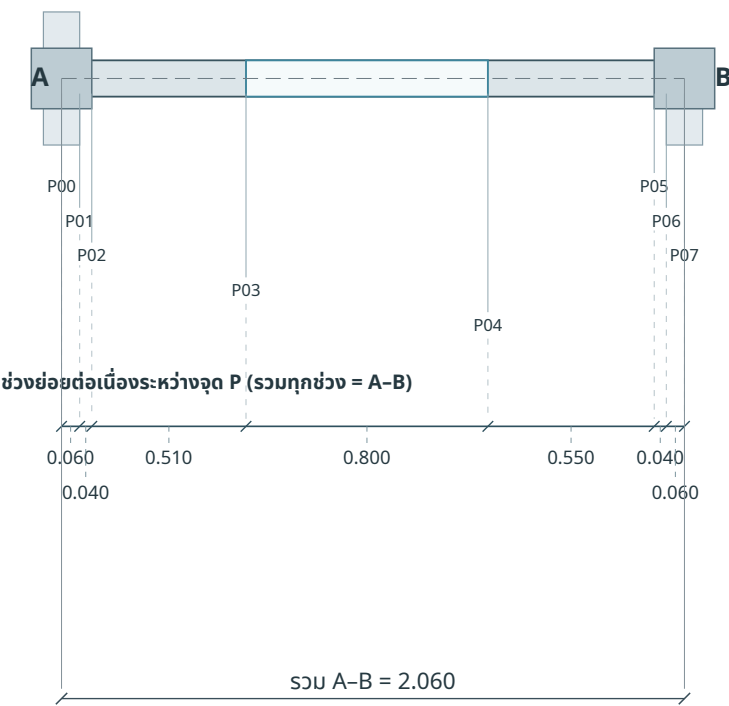

รูปด้านคลี่ A→B / 1:50

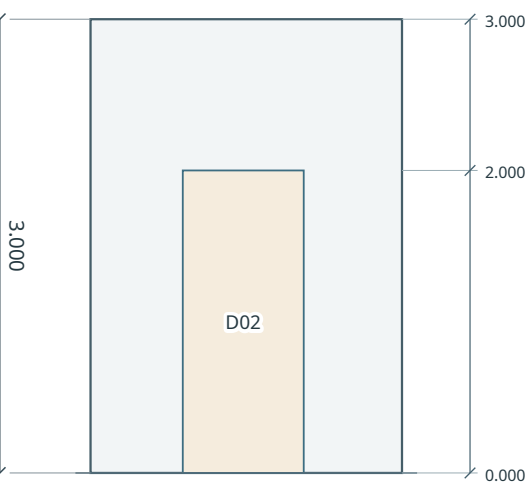

ช่องเปิด: กว้าง×สูง | A→ขอบแรก / ขอบท้าย→B | ขอบล่าง / หัวช่อง

D02 0.800×2.000 | 0.610/0.650 | 0.000/2.000

จุด	จาก A	ช่วงย่อ	ตำแหน่ง / เหตุการณ์
P00	0.000	—	A / J11 / J12 / J13 / C4
P01	0.060	0.060	J11+ / J12+
P02	0.100	0.040	C4+
P03	0.610	0.510	D02L
P04	1.410	0.800	D02R
P05	1.960	0.550	C7-
P06	2.000	0.040	J16-
P07	2.060	0.060	B / J15 / J16 / C7

รวมช่วงย่อ 2.060 ม.

ตำแหน่งจาก A ที่อยู่นอก A-B (ไม่นับรวม)

C4- -0.100 ม.	J11- -0.060 ม.
J12- -0.060 ม.	J16+ 2.120 ม.
C7+ 2.160 ม.	


OHM HOUSE

WL15 / ระยะย่อทุกจุด


ผังขยาย 1:50 • รูปด้านคลี่ 1:50 • ระยะทั้งหมดเป็นเมตร • ยาว 7.880 / สูง 3.000 / หน้า 0.120

A (5.500, 5.000) → B (5.500, 12.880) ในแกน (X,Z)

ผังขยายตามแกน A→B / 1:50

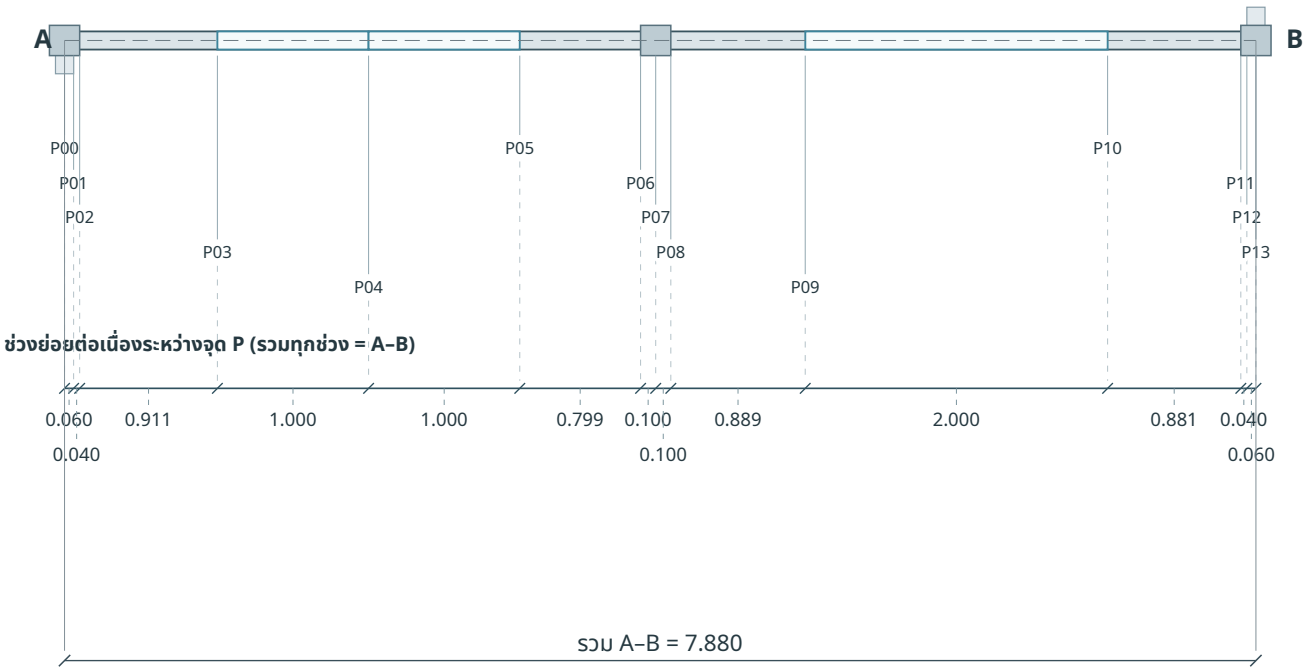

รูปด้านคลี่ A→B / 1:50

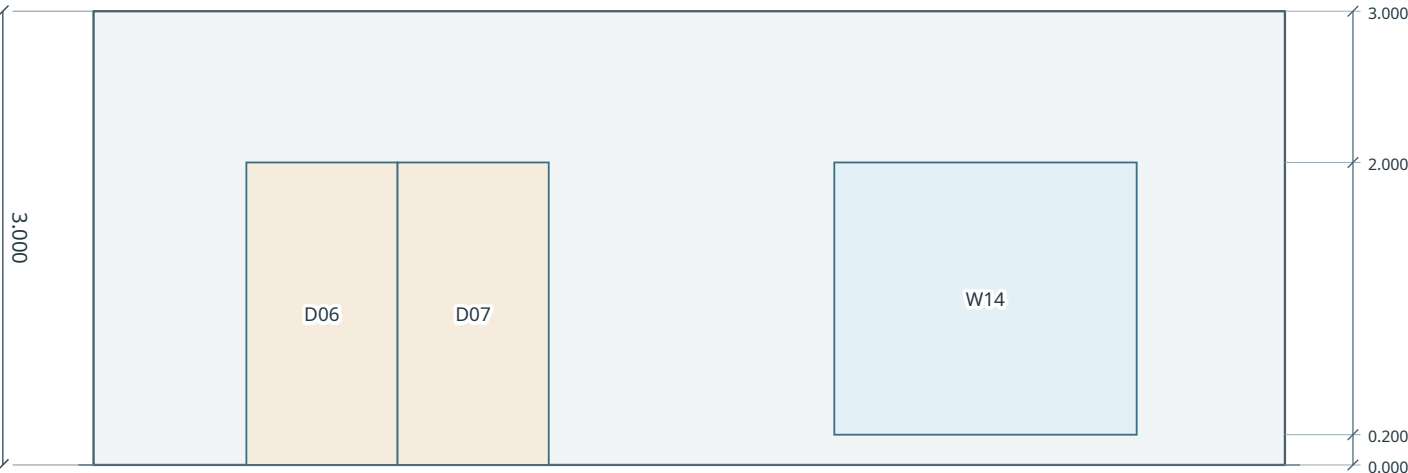

ช่องเปิด: กว้าง×สูง | A→ขอบแรก / ขอบท้าย→B | ขอบล่าง / หัวช่อง

D06 1.000×2.000 1.011/5.869 0.000/2.000	D07 1.000×2.000 2.011/4.869 0.000/2.000
W14 2.000×1.800 4.899/0.981 0.200/2.000	

จุด	จาก A	ช่วงย่อย	ตำแหน่ง / เหตุการณ์
P00	0.000	—	A / J14 / J16 / C7
P01	0.060	0.060	J16+
P02	0.100	0.040	C7+
P03	1.011	0.911	D06L
P04	2.011	1.000	D07L / D06R
P05	3.011	1.000	D07R
P06	3.810	0.799	C15-
P07	3.910	0.100	C15
P08	4.010	0.100	C15+
P09	4.899	0.889	W14L
P10	6.899	2.000	W14R
P11	7.780	0.881	C13-
P12	7.820	0.040	J07-
P13	7.880	0.060	B / J07 / C13

รวมช่วงย่อย 7.880 ม.

ตำแหน่งจาก A ที่อยู่นอก A-B (ไม่นับรวม)

C7- -0.100 ม.	J16- -0.060 ม.
J07+ 7.940 ม.	C13+ 7.980 ม.


OHM HOUSE

WL16 / ระยะย่อทุกจุด

ผังขยาย 1:25 • รูปด้านคลี่ 1:50 • ระยะทั้งหมดเป็นเมตร • ยาว 3.000 / สูง 3.000 / หน้า 0.120

A (2.500, 5.000) → B (5.500, 5.000) ในแกน (X,Z)

ผังขยายตามแกน A→B / 1:25

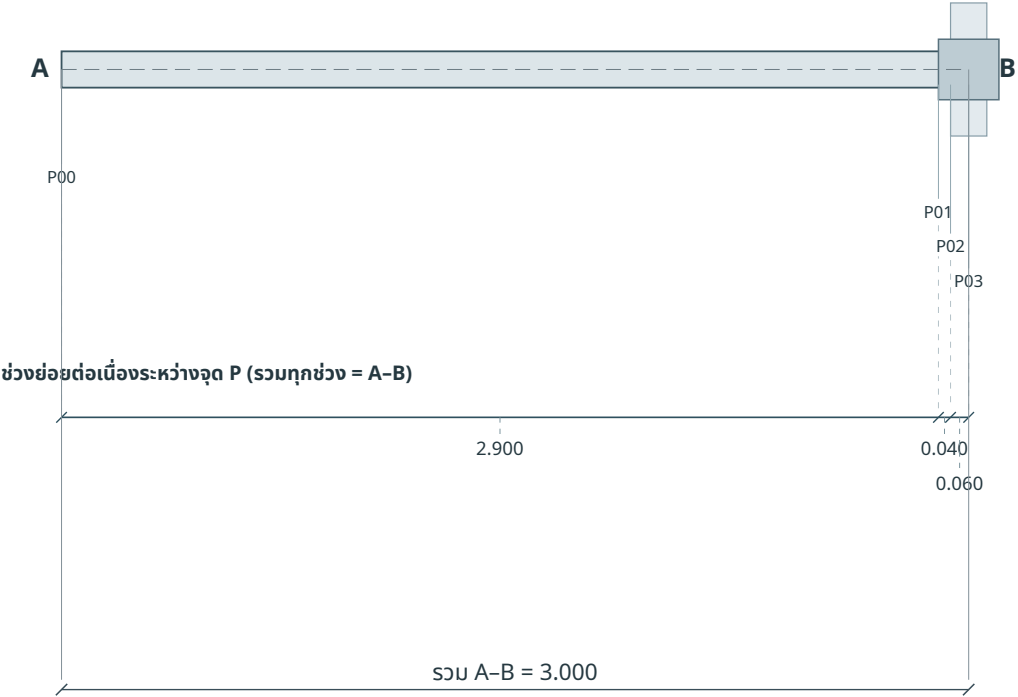

รูปด้านคลี่ A→B / 1:50



ช่องเปิด: กว้าง×สูง | A→ขอบแรก / ขอบท้าย→B | ขอบล่าง / หัวช่อง

ไม่มีช่องเปิดในผนังแบบนี้ตามไฟล์

จุด	จาก A	ช่วงย่อย	ตำแหน่ง / เหตุการณ์
P00	0.000	—	A / J08
P01	2.900	2.900	C7-
P02	2.940	0.040	J14- / J15-
P03	3.000	0.060	B / J14 / J15 / C7

รวมช่วงย่อย 3.000 ม.

ตำแหน่งจาก A ที่อยู่นอก A-B (ไม่นับรวม)

J14+ 3.060 ม.

J15+ 3.060 ม.

C7+ 3.100 ม.


OHM HOUSE

WL17 / ระยะย่อทุกจุด


ผังขยาย 1:25 • รูปด้านคลี่ 1:50 • ระยะทั้งหมดเป็นเมตร • ยาว 2.940 / สูง 3.000 / หน้า 0.120

A (7.500, 0.000) → B (7.500, 2.940) ในแกน (X,Z)

ผังขยายตามแกน A→B / 1:25

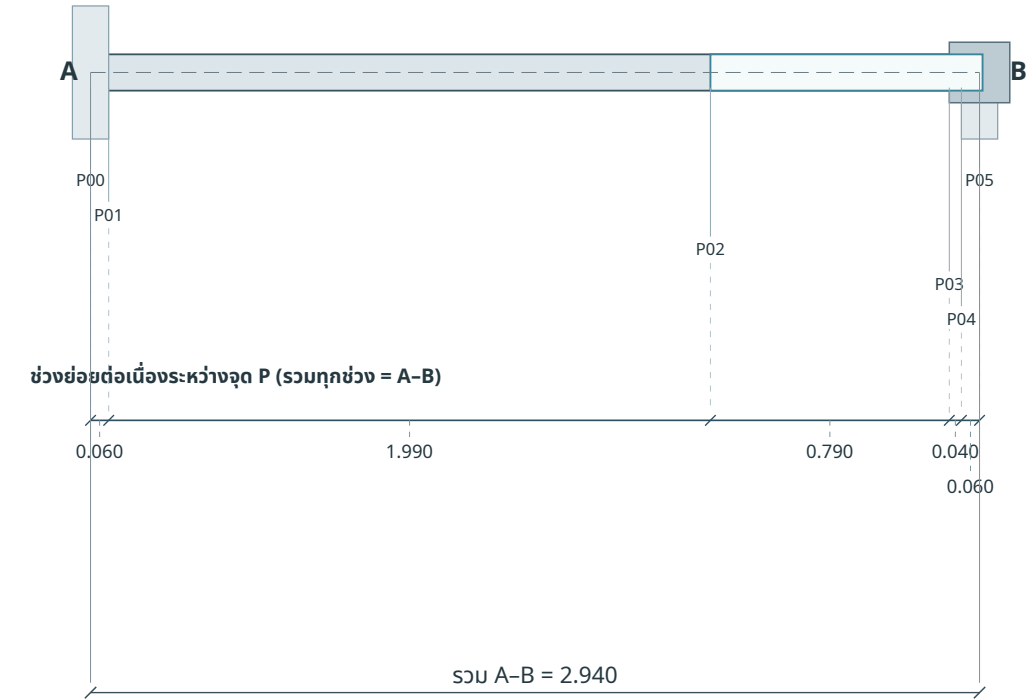

รูปด้านคลี่ A→B / 1:50

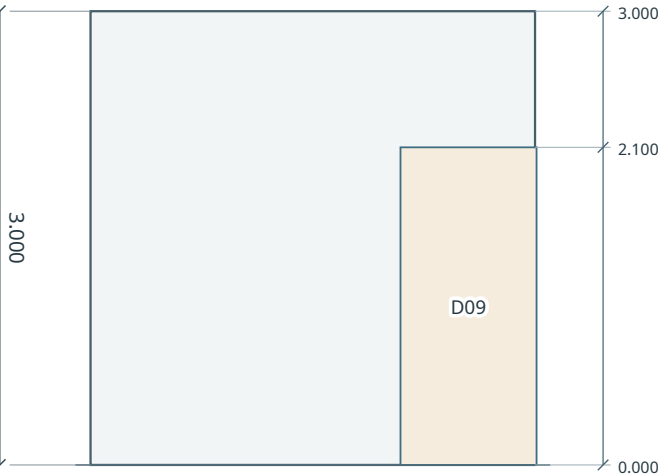

ช่องเปิด: กว้าง×สูง | A→ขอบแรก / ขอบท้าย→B | ขอบล่าง / หัวช่อง

D09 0.900×2.100 | 2.050/-0.010 | 0.000/2.100

จุด	จาก A	ช่วงย่อย	ตำแหน่ง / เหตุการณ์
P00	0.000	—	A / J01
P01	0.060	0.060	J01+
P02	2.050	1.990	D09L
P03	2.840	0.790	C5-
P04	2.880	0.040	J12-
P05	2.940	0.060	B / J12 / J18 / C5

รวมช่วงย่อย 2.940 ม.

ตำแหน่งจาก A ที่อยู่นอก A-B (ไม่นับรวม)

J01- -0.060 ม.

D09R 2.950 ม.

J12+ 3.000 ม.

C5+ 3.040 ม.

D09R เกินปลาย B 0.010 ม. ต้องตรวจแก้


OHM HOUSE

WL18 / ระยะย่อทุกจุด


ผังขยาย 1:25 • รูปด้านคลี่ 1:50 • ระยะทั้งหมดเป็นเมตร • ยาว 2.060 / สูง 3.000 / หน้า 0.120

A (7.500, 2.940) → B (7.500, 5.000) ในแกน (X,Z)

ผังขยายตามแกน A→B / 1:25

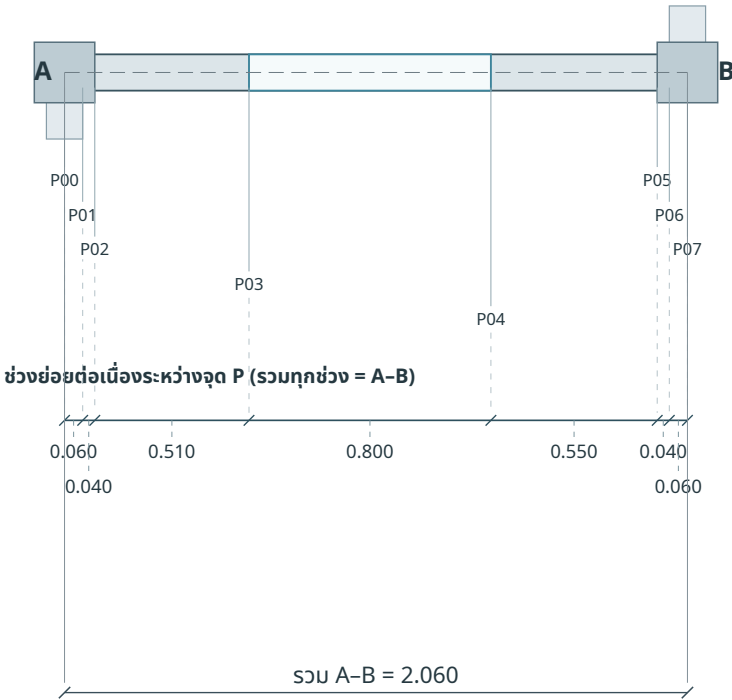

รูปด้านคลี่ A→B / 1:50

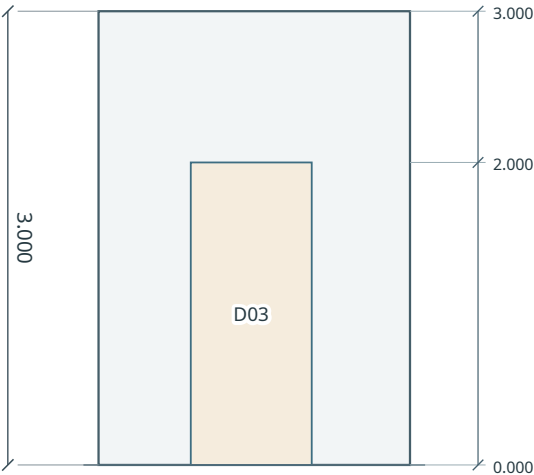

ช่องเปิด: กว้าง×สูง | A→ขอบแรก / ขอบท้าย→B | ขอบล่าง / หัวช่อง

D03 0.800×2.000 | 0.610/0.650 | 0.000/2.000

จุด	จาก A	ช่วงย่อย	ตำแหน่ง / เหตุการณ์
P00	0.000	—	A / J12 / J17 / C5
P01	0.060	0.060	J12+
P02	0.100	0.040	C5+
P03	0.610	0.510	D03L
P04	1.410	0.800	D03R
P05	1.960	0.550	C8-
P06	2.000	0.040	J19-
P07	2.060	0.060	B / J19 / C8

รวมช่วงย่อย 2.060 ม.

ตำแหน่งจาก A ที่อยู่นอก A-B (ไม่นับรวม)

C5- -0.100 ม. J12- -0.060 ม.
J19+ 2.120 ม. C8+ 2.160 ม.


OHM HOUSE

WL19 / ระยะย่อทุกจุด

ผังขยาย 1:25 • รูปด้านคลี่ 1:50 • ระยะทั้งหมดเป็นเมตร • ยาว 3.500 / สูง 3.000 / หน้า 0.120

A (7.500, 5.000) → B (11.000, 5.000) ในแกน (X,Z)

ผังขยายตามแกน A→B / 1:25

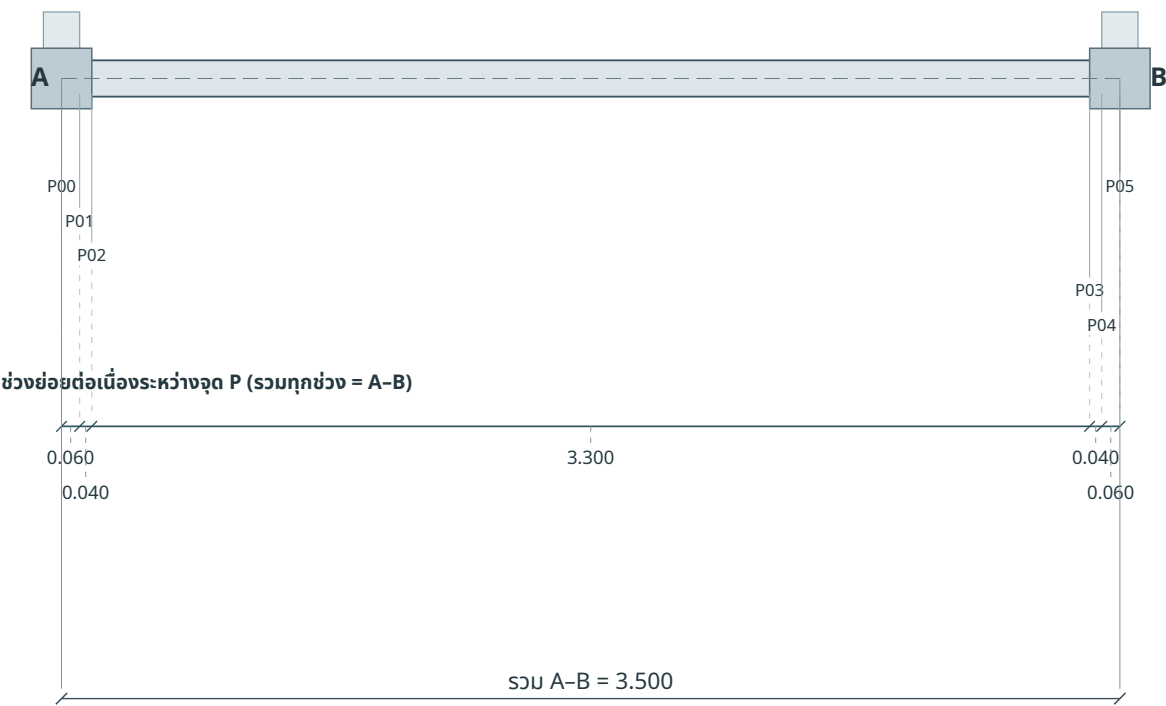

ช่วงย่อยต่อเนื่องระหว่างจุด P (รวมทุกช่วง = A-B)

0,060 3,300 0,040 0,060

รูปด้านคลี่ A→B / 1:50



ช่องเปิด: กว้าง×สูง | A→ขอบแรก / ขอบท้าย→B | ขอบล่าง / หัวช่อง

ไม่มีช่องเปิดในผนังแนวนอนนี้ตามไฟล์

จุด	จาก A	ช่วงย่อย	ตำแหน่ง / เหตุการณ์
P00	0.000	—	A / J18 / C8
P01	0.060	0.060	J18+
P02	0.100	0.040	C8+
P03	3.400	3.300	C9-
P04	3.440	0.040	J02-
P05	3.500	0.060	B / J02 / J03 / C9

รวมช่วงย่อย 3.500 ม.

ตำแหน่งจาก A ที่อยู่นอก A-B (ไม่นับรวม)

C8- -0.100 ม. J18- -0.060 ม.
J02+ 3.560 ม. C9+ 3.600 ม.


OHM HOUSE

WL20 / ระยะย่อทุกจุด


ผังขยาย 1:25 • รูปด้านคลี่ 1:50 • ระยะทั้งหมดเป็นเมตร • ยาว 1.790 / สูง 3.000 / หน้า 0.120

A (11.000, 7.440) → B (12.790, 7.440) ในแกน (X,Z)

ผังขยายตามแกน A→B / 1:25

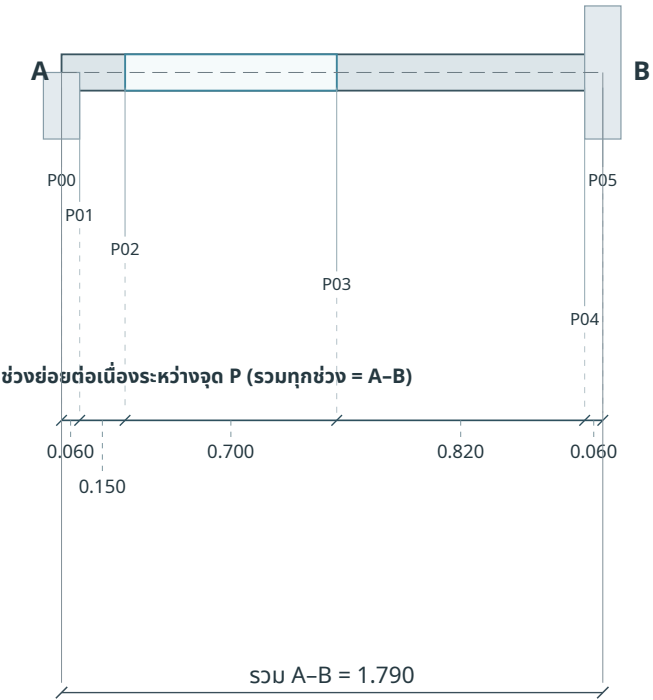

รูปด้านคลี่ A→B / 1:50

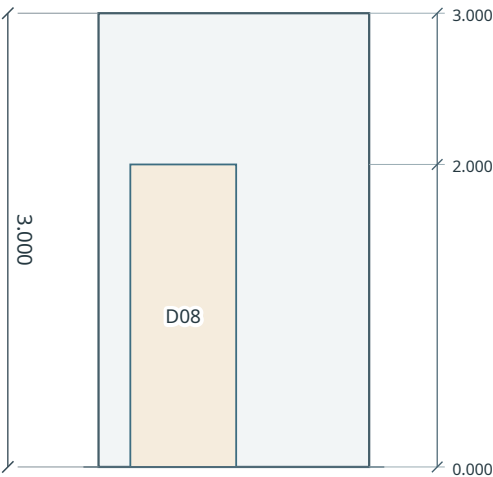

ช่องเปิด: กว้าง×สูง | A→ขอบแรก / ขอบท้าย→B | ขอบล่าง / หัวช่อง

D08 0.700×2.000 | 0.210/0.880 | 0.000/2.000

จุด	จาก A	ช่วงย่อย	ตำแหน่ง / เหตุการณ์
P00	0.000	—	A / J21
P01	0.060	0.060	J21+
P02	0.210	0.150	D08L
P03	0.910	0.700	D08R
P04	1.730	0.820	J04-
P05	1.790	0.060	B / J04

รวมช่วงย่อย 1.790 ม.

ตำแหน่งจาก A ที่อยู่นอก A-B (ไม่นับรวม)

J21 - -0.060 ม.

J04 + 1.850 ม.


OHM HOUSE

WL21 / ระยะย่อทุกจุด


ผังขยาย 1:25 • รูปด้านคลี่ 1:50 • ระยะทั้งหมดเป็นเมตร • ยาว 1.940 / สูง 3.000 / หน้า 0.120

A (11.000, 7.440) → B (11.000, 9.380) ในแกน (X,Z)

ผังขยายตามแกน A→B / 1:25

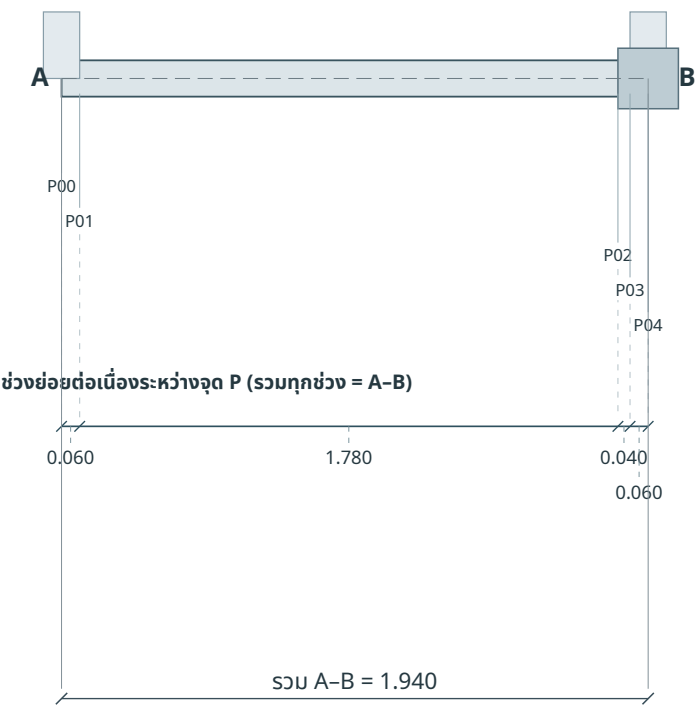

รูปด้านคลี่ A→B / 1:50

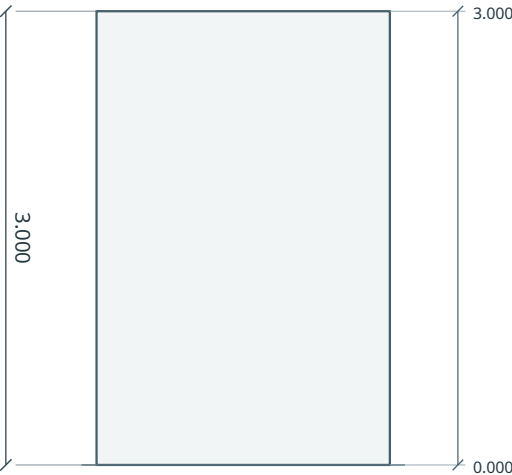

ช่องเปิด: กว้าง×สูง | A→ขอบแรก / ขอบท้าย→B | ขอบล่าง / หัวช่อง

ไม่มีช่องเปิดในผนังแบบนี้ตามไฟล์

จุด	จาก A	ช่วงย่อย	ตำแหน่ง / เหตุการณ์
P00	0.000	—	A / J20
P01	0.060	0.060	J20+
P02	1.840	1.780	C11-
P03	1.880	0.040	J05-
P04	1.940	0.060	B / J05 / J06 / C11

รวมช่วงย่อย 1.940 ม.

ตำแหน่งจาก A ที่อยู่นอก A-B (ไม่นับรวม)

J20- -0.060 ม. J05+ 2.000 ม.

C11+ 2.040 ม.