


OHM HOUSE

แปลนรวม / ระยะรอบบ้าน

มาตราส่วน 1:75 • ขนาดรวมและทุกช่วงขอบพื้น • ไม่รวมชายคาหลังคา

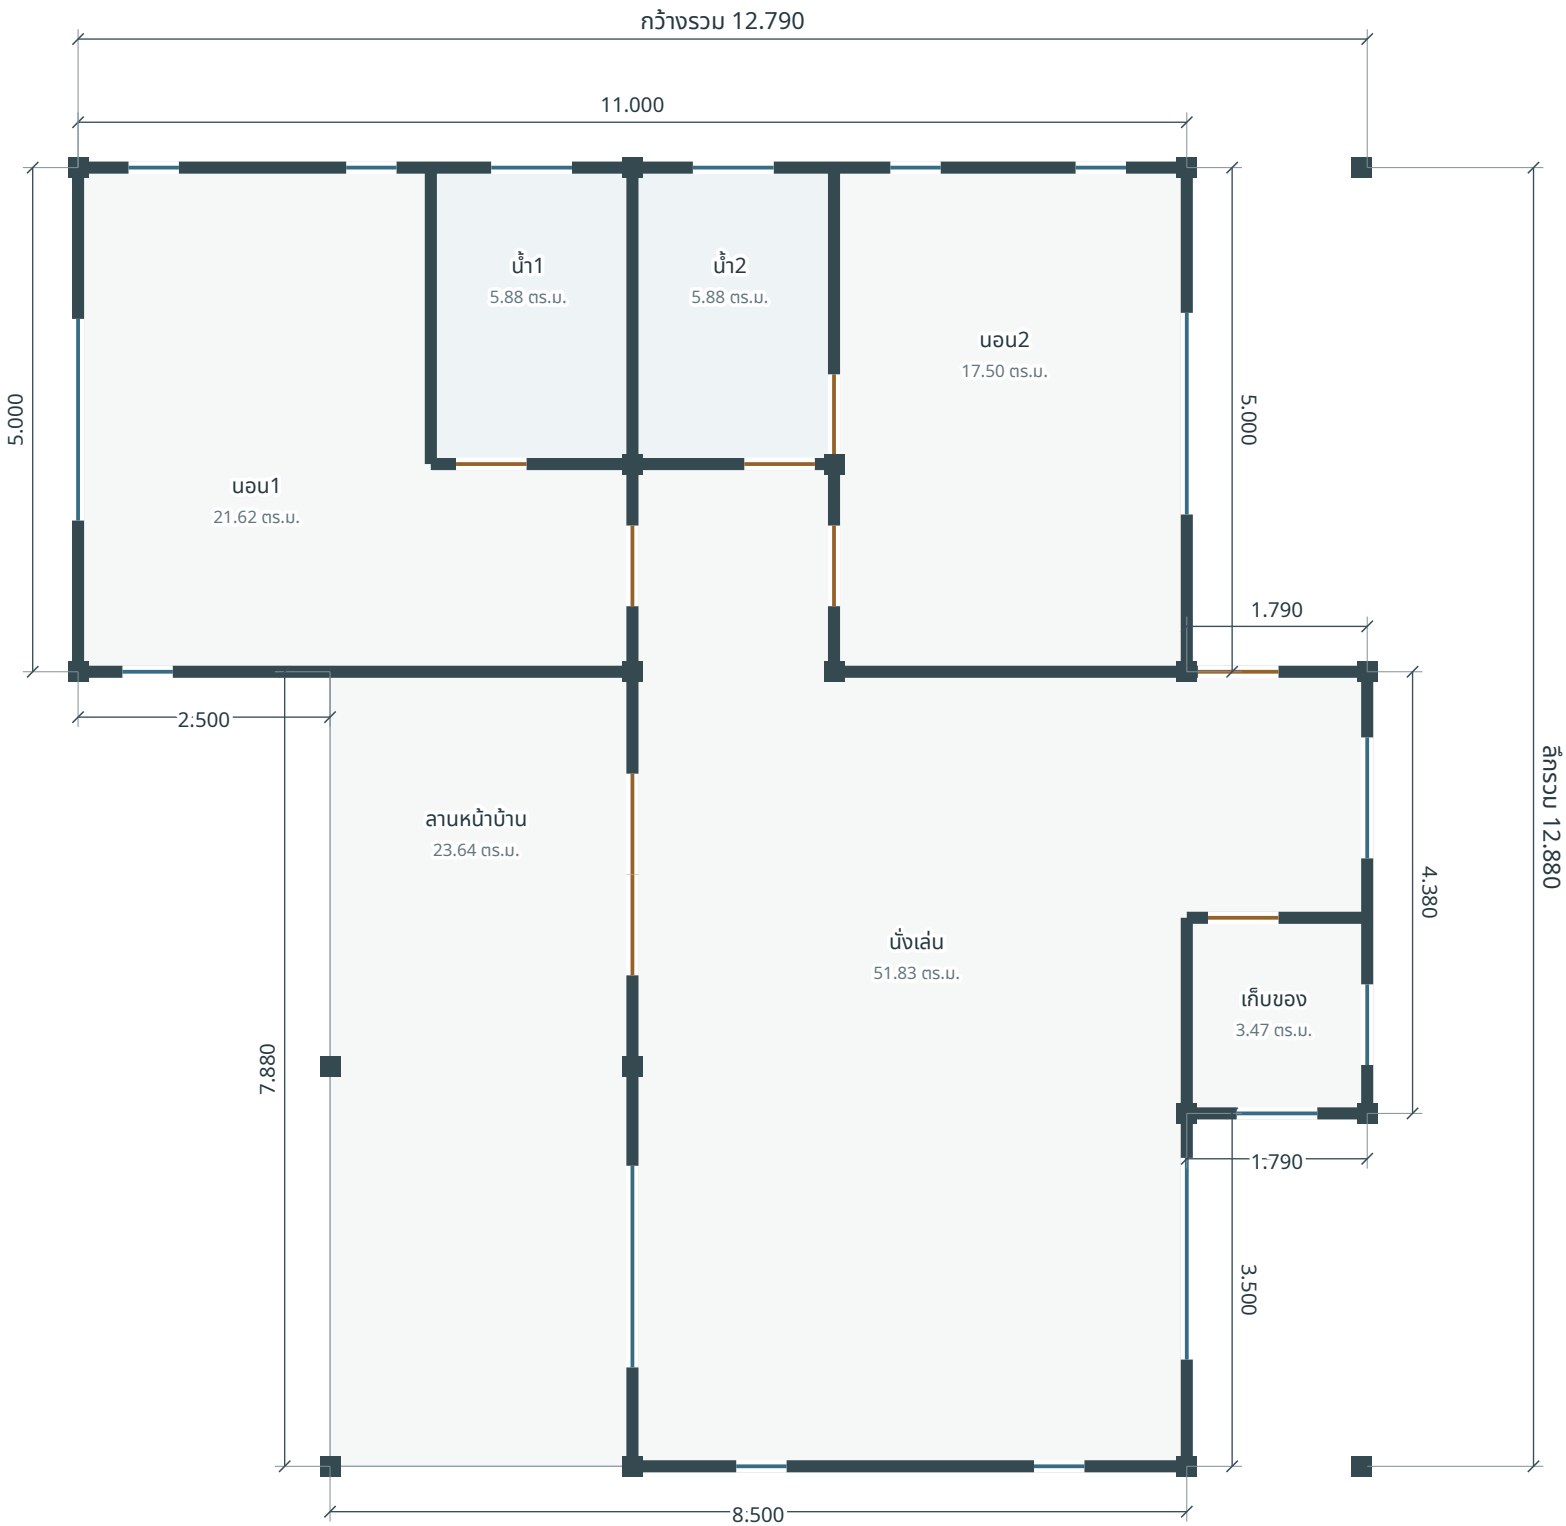

ขนาดอ้างอิง

กว้างรวม	12.790 ม.
ลึกรวม	12.880 ม.
พื้นที่ขอบพื้น	129.82 ตร.ม.

แผ่นในชุดนี้


- A-01 แปลนรวม / ระยะขอบพื้น
- A-02 แกนผนัง / ความยาว สูง หน้า
- A-03 ระยะห้องนอนและห้องน้ำ
- A-04 ระยะห้องนั่งเล่น ลาน และเก็บของ
- A-05 ตำแหน่งประตู-หน้าต่าง
- A-06 ตารางขนาดช่องเปิดครบทุกระยะ

อ่านแบบก่อนใช้งาน

- บ้านมีส่วนเข้า ไม่ใช่สี่เหลี่ยมเต็ม
- พื้นที่ห้องยังไม่หักผนังและผิวฉาบ
- ผังใช้แกน X → และ Z ↓ ตามไฟล์
- ในข้อมูลไม่มีทิศเหนือ จึงไม่กำหนดเพิ่ม
- ขอบพื้นไม่ใช่แนวชายคาหรือแนวเขตที่ดิน



แบบเวกเตอร์: ชุมได้โดยเส้นไม่แตก

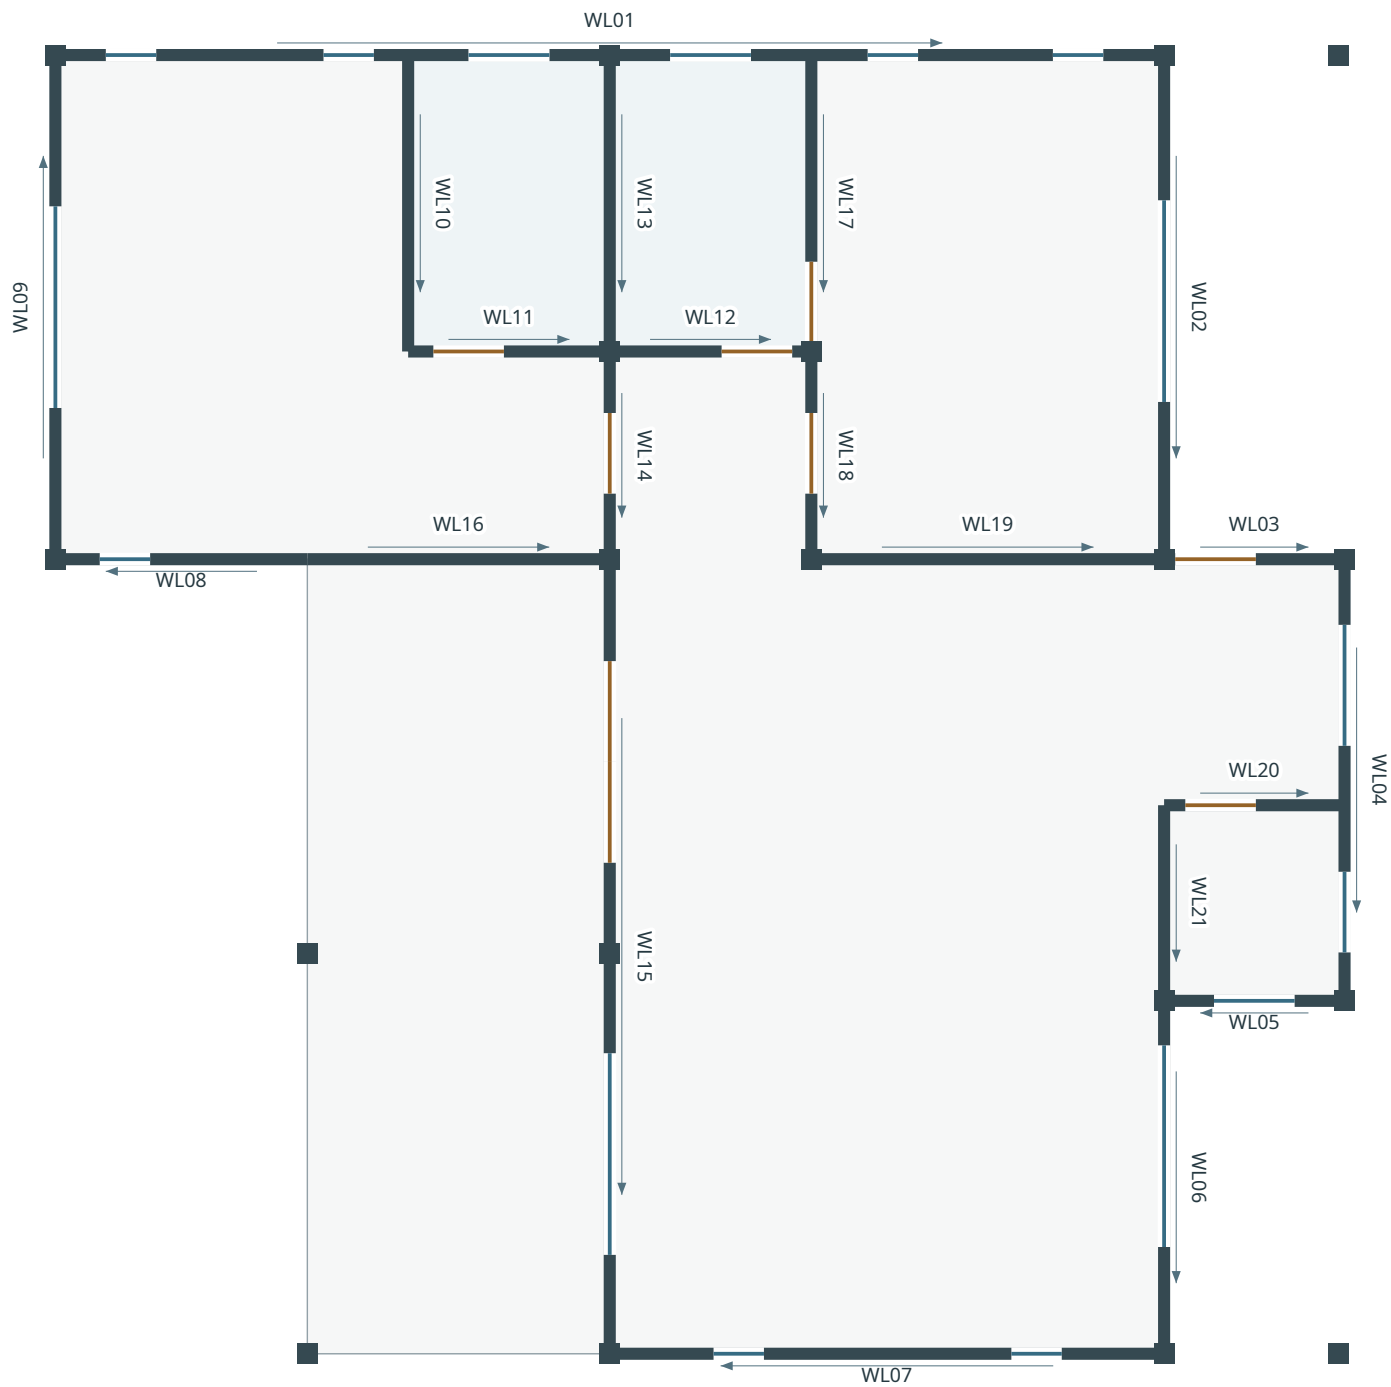

ตารางผนังครบ 21 แนว

ผนัง	ยาว A-B	สูง	หนา
WL01	11.000	3.000	0.120
WL02	5.000	3.000	0.120
WL03	1.790	3.000	0.120
WL04	4.380	3.000	0.120
WL05	1.790	3.000	0.120
WL06	3.500	3.000	0.120
WL07	5.500	3.000	0.120
WL08	2.500	3.000	0.120
WL09	5.000	3.000	0.120
WL10	2.940	3.000	0.120
WL11	2.000	3.000	0.120
WL12	2.000	3.000	0.120
WL13	2.940	3.000	0.120
WL14	2.060	3.000	0.120
WL15	7.880	3.000	0.120
WL16	3.000	3.000	0.120
WL17	2.940	3.000	0.120
WL18	2.060	3.000	0.120
WL19	3.500	3.000	0.120
WL20	1.790	3.000	0.120
WL21	1.940	3.000	0.120

ระยะทั้งหมดเป็นเมตร

A = ชั้นแกนผนัง / B = ปลายแกนผนัง

อ่านทิศ A→B ตามลูกศรของแต่ละผนัง

ความยาวยังไม่ใช้ระยะสุกหลั้งฉาบ


มาตราส่วน 1:75 • แถบสเกล 0-5 เมตร



OHM HOUSE

ระยะห้อง / ห้องนอนและห้องน้ำ


มาตราส่วน 1:75 ทุกภาพ • แยกห้องเพื่ออ่านทุกช่วงขอบได้ชัด • ตำแหน่งภาพไม่ใช่ผังรวม

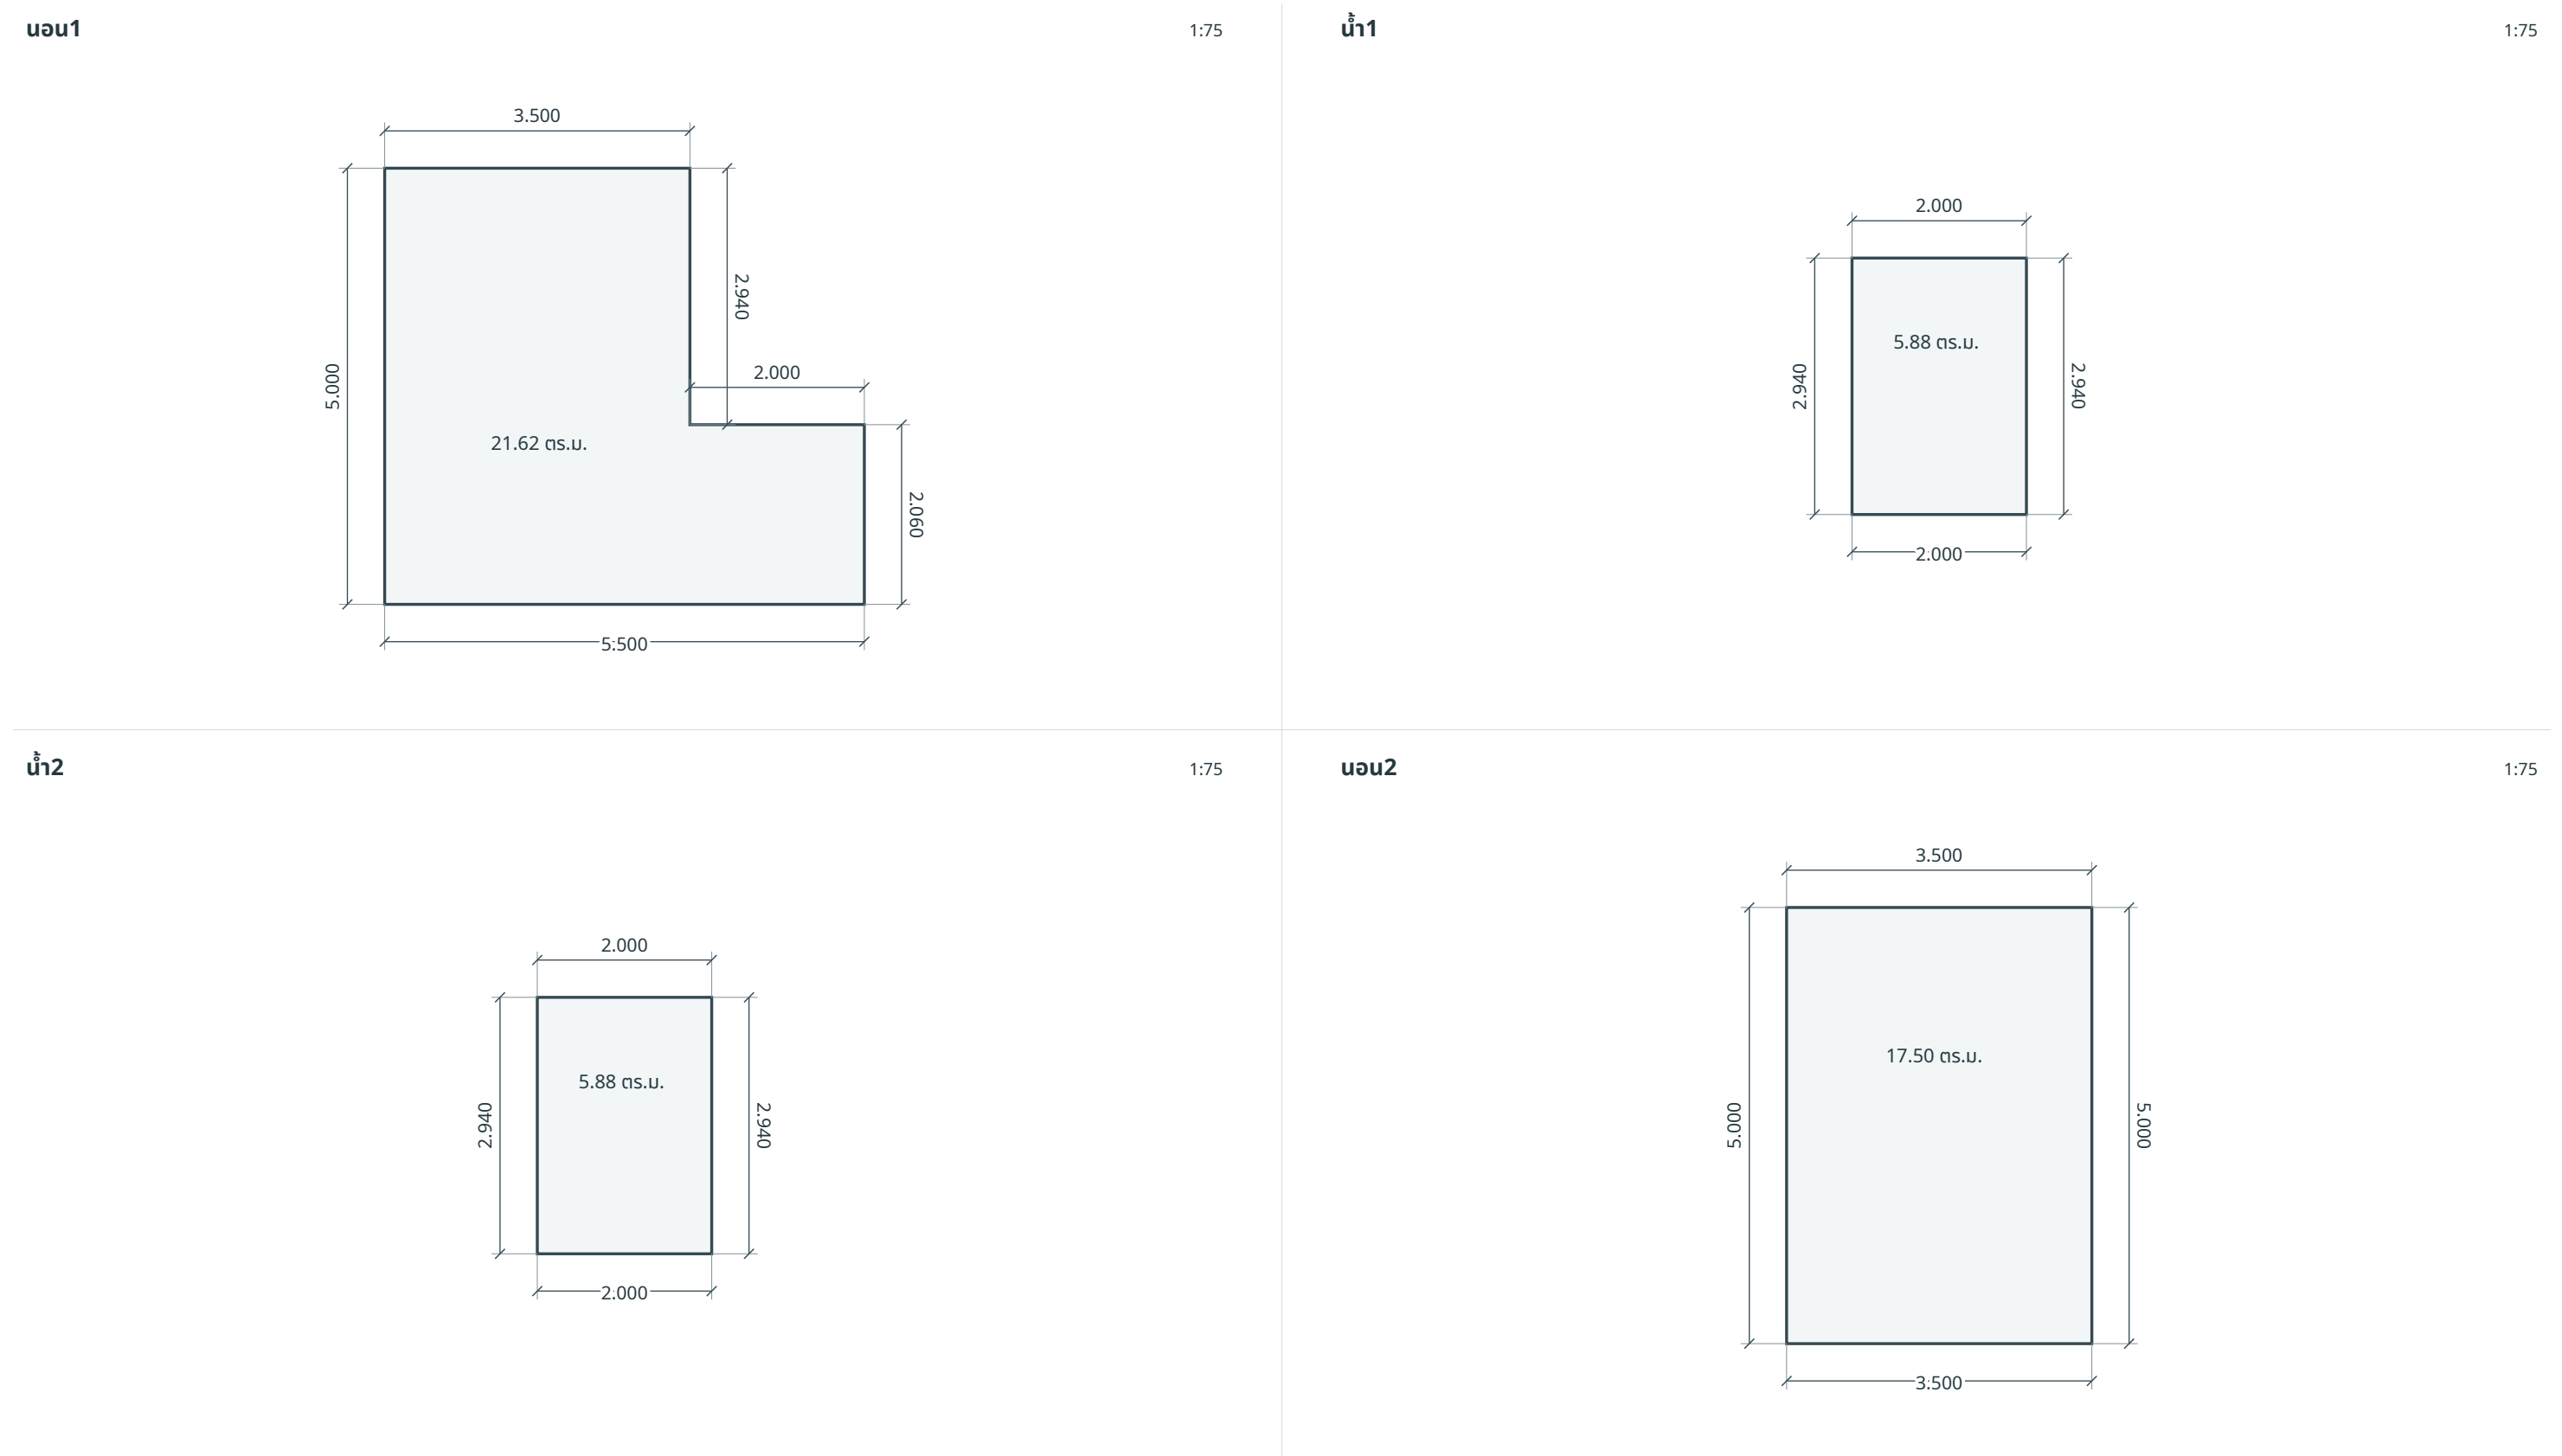

OHM HOUSE

ระยะห้อง / นั่งเล่น ลาน และเก็บของ

มาตราส่วน 1:75 ทุกภาพ • ห้องรูปตัว L แสดงระยะแยกทุกช่วง • ไม่ใช้กรอบสี่เหลี่ยมแทนพื้นที่จริง

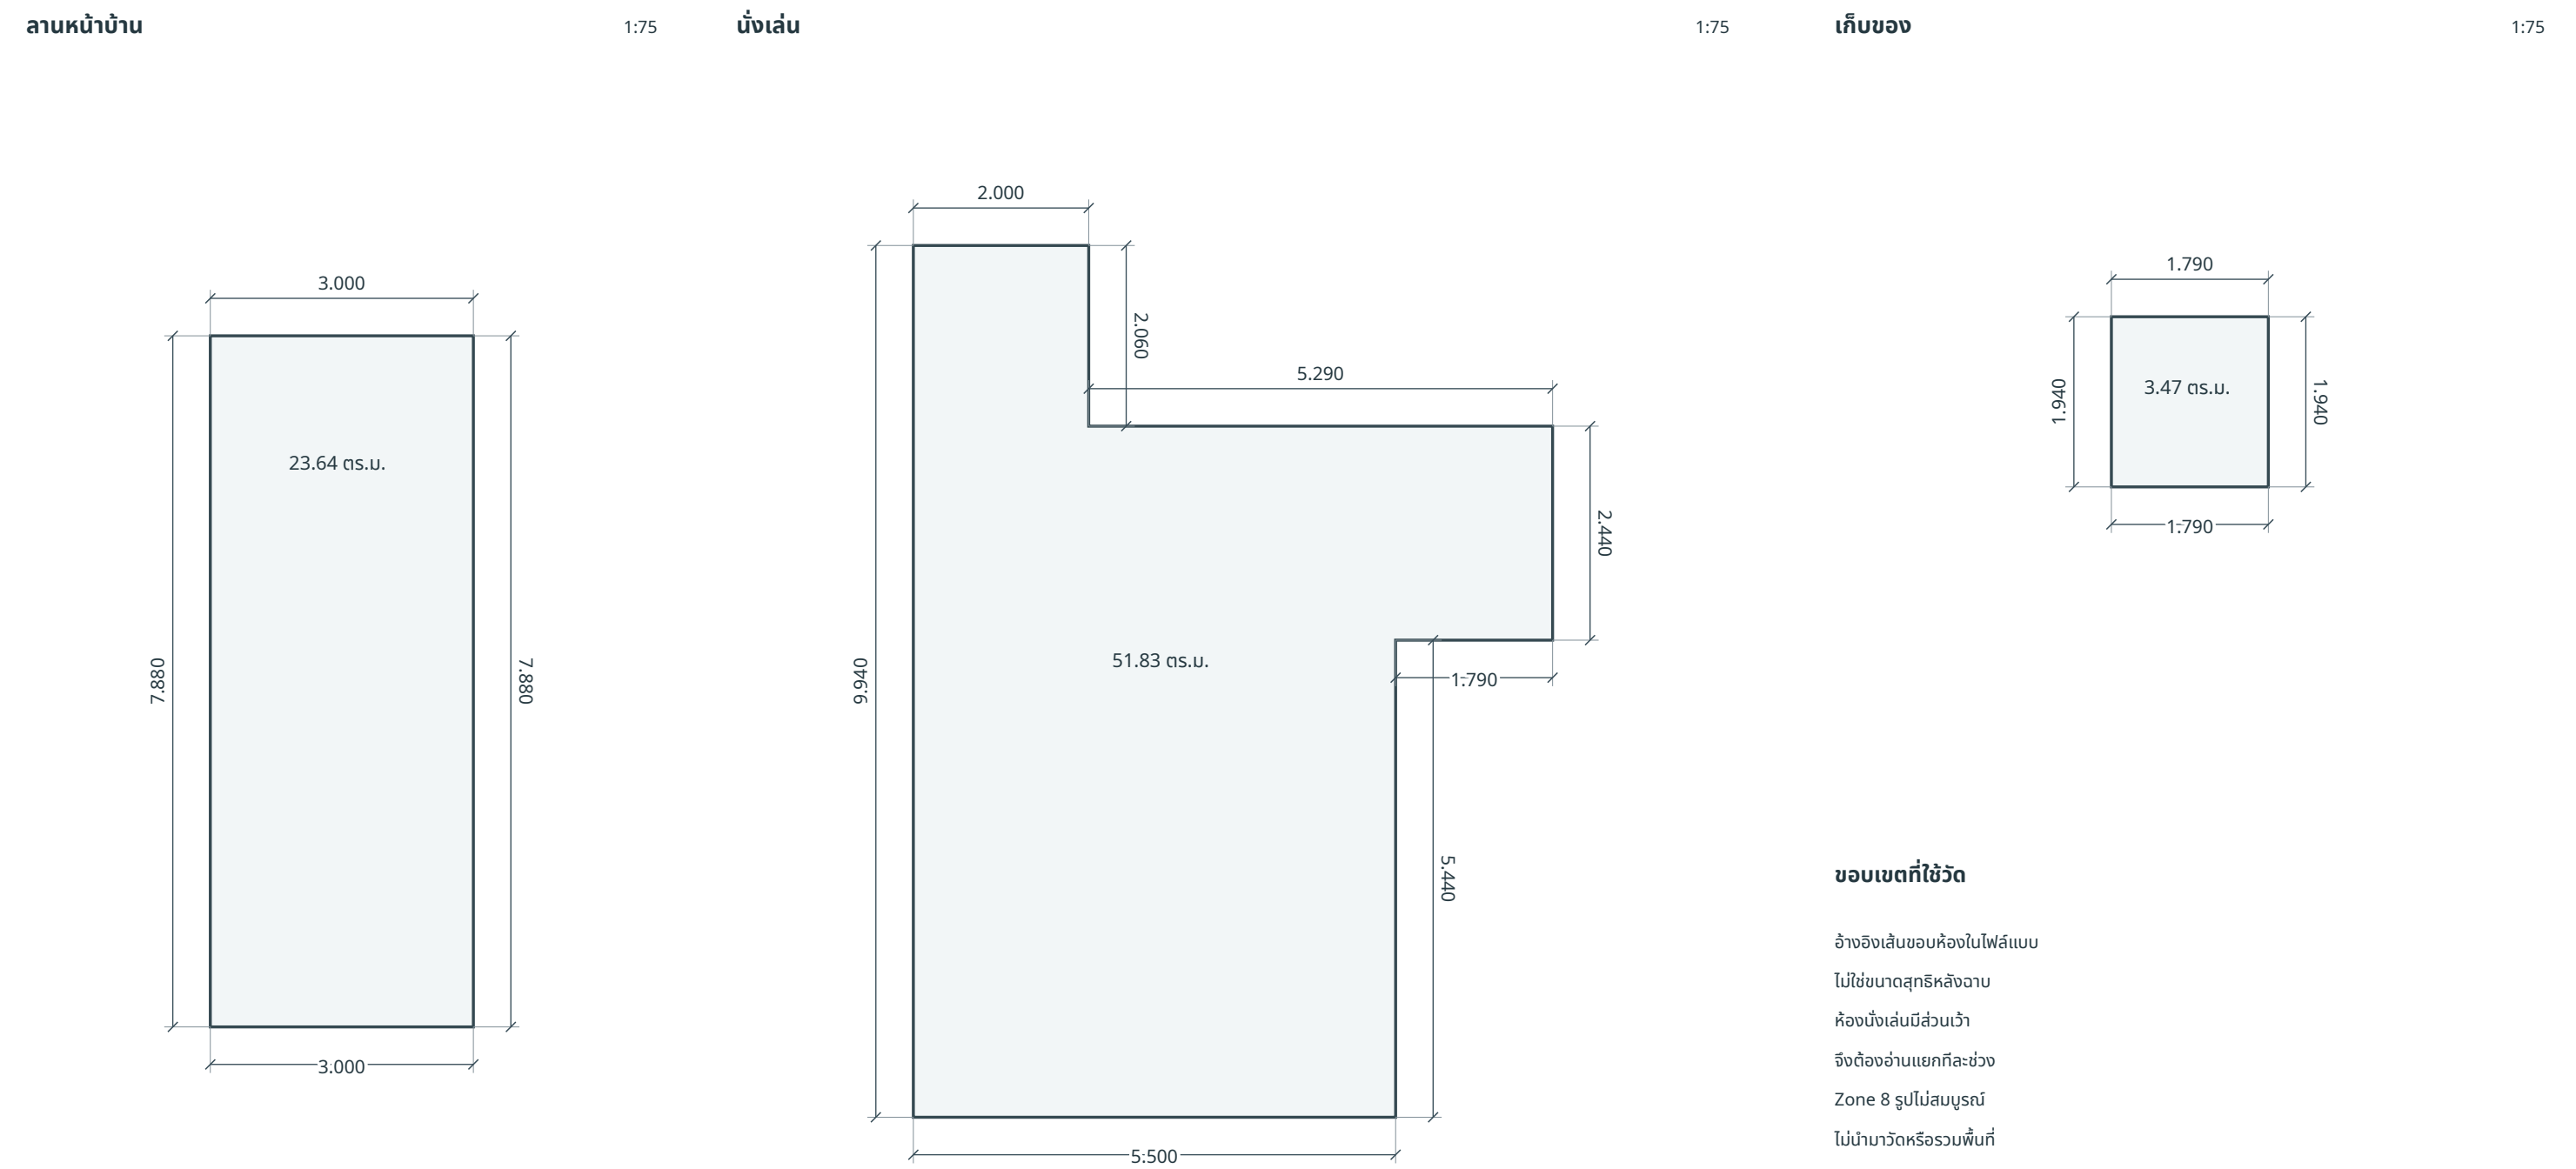

OHM HOUSE

ประตู-หน้าต่าง / ตำแหน่งตามแนวมผนัง

มาตราส่วน 1:75 • D = ประตู / W = หน้าต่าง • ใช้ทิศแทน A→B ของแผ่น A-02



มาตราส่วน 1:75 • แถบสเกล 0-5 เมตร



ระยะตามแกนผนัง (เมตร)

รหัส	ผนัง	A→ขอบแรก	กว้าง	ขอบท้าย→B
D01	WL03	0.110	0.800	0.880
D02	WL14	0.610	0.800	0.650
D03	WL18	0.610	0.800	0.650
D04	WL11	0.250	0.700	1.050
D05	WL12	1.110	0.700	0.190
D06	WL15	1.011	1.000	5.869
D07	WL15	2.011	1.000	4.869
D08	WL20	0.210	0.700	0.880
D09	WL17	2.050	0.900	-0.010
W01	WL01	2.660	0.500	7.840
W02	WL01	4.100	0.800	6.100
W03	WL01	6.100	0.800	4.100
W04	WL01	8.059	0.500	2.441
W05	WL01	9.897	0.500	0.603
W06	WL09	1.500	2.000	1.500
W07	WL02	1.440	2.000	1.560
W08	WL08	1.560	0.500	0.440
W09	WL04	0.651	1.200	2.529
W10	WL07	3.970	0.500	1.030
W11	WL07	1.015	0.500	3.985
W12	WL06	0.441	2.000	1.059
W13	WL05	0.495	0.800	0.495
W14	WL15	4.899	2.000	0.981
W15	WL04	3.100	0.800	0.480
W16	WL01	4.101	0.800	6.099
W17	WL01	6.100	0.800	4.100
W18	WL01	0.501	0.500	9.999

D09: ขอบช่องเกินปลายผนัง 0.010 ม.

ค่าลบแสดงตามไฟล์ ไม่ปรับเป็นศูนย์

A→ขอบแรก + กว้าง + ขอบท้าย→B = ยาวผนัง

OHM HOUSE

ตารางขนาดช่องเปิด / ระยะครบทุกจุด

ตารางข้อมูล หน่วยเมตร • ไม่ใช้สเกลวัดจากตาราง • ระดับแนวตั้งอ้างอิงพื้นผนังในแบบ = ±0.000

รหัส	ชนิด	ผนัง	กว้าง	สูง	A→ขอบแรก	ขอบท้าย→B	ขอบล่าง	หัวช่อง	สถานะ
D01	ประตู	WL03	0.800	2.000	0.110	0.880	0.000	2.000	ตามไฟล์แบบ
D02	ประตู	WL14	0.800	2.000	0.610	0.650	0.000	2.000	ตามไฟล์แบบ
D03	ประตู	WL18	0.800	2.000	0.610	0.650	0.000	2.000	ตามไฟล์แบบ
D04	ประตู	WL11	0.700	2.000	0.250	1.050	0.000	2.000	ตามไฟล์แบบ
D05	ประตู	WL12	0.700	2.000	1.110	0.190	0.000	2.000	ตามไฟล์แบบ
D06	ประตู	WL15	1.000	2.000	1.011	5.869	0.000	2.000	ตามไฟล์แบบ
D07	ประตู	WL15	1.000	2.000	2.011	4.869	0.000	2.000	ตามไฟล์แบบ
D08	ประตู	WL20	0.700	2.000	0.210	0.880	0.000	2.000	ตามไฟล์แบบ
D09	ประตู	WL17	0.900	2.100	2.050	-0.010	0.000	2.100	เกินผนัง 0.010 ม.
W01	หน้าต่าง	WL01	0.500	1.500	2.660	7.840	0.750	2.250	ตามไฟล์แบบ
W02	หน้าต่าง	WL01	0.800	0.500	4.100	6.100	1.750	2.250	ตามไฟล์แบบ
W03	หน้าต่าง	WL01	0.800	0.500	6.100	4.100	1.750	2.250	ตามไฟล์แบบ
W04	หน้าต่าง	WL01	0.500	1.500	8.059	2.441	0.750	2.250	ตามไฟล์แบบ
W05	หน้าต่าง	WL01	0.500	1.500	9.897	0.603	0.750	2.250	ตามไฟล์แบบ
W06	หน้าต่าง	WL09	2.000	1.200	1.500	1.500	0.900	2.100	ตามไฟล์แบบ
W07	หน้าต่าง	WL02	2.000	1.200	1.440	1.560	0.900	2.100	ตามไฟล์แบบ
W08	หน้าต่าง	WL08	0.500	1.500	1.560	0.440	0.750	2.250	ตามไฟล์แบบ
W09	หน้าต่าง	WL04	1.200	1.200	0.651	2.529	0.900	2.100	ตามไฟล์แบบ
W10	หน้าต่าง	WL07	0.500	1.500	3.970	1.030	0.750	2.250	ตามไฟล์แบบ
W11	หน้าต่าง	WL07	0.500	1.500	1.015	3.985	0.750	2.250	ตามไฟล์แบบ
W12	หน้าต่าง	WL06	2.000	1.800	0.441	1.059	0.200	2.000	ตามไฟล์แบบ
W13	หน้าต่าง	WL05	0.800	0.500	0.495	0.495	1.550	2.050	ตามไฟล์แบบ
W14	หน้าต่าง	WL15	2.000	1.800	4.899	0.981	0.200	2.000	ตามไฟล์แบบ
W15	หน้าต่าง	WL04	0.800	0.500	3.100	0.480	1.750	2.250	ตามไฟล์แบบ
W16	หน้าต่าง	WL01	0.800	0.500	4.101	6.099	2.250	2.750	ตามไฟล์แบบ
W17	หน้าต่าง	WL01	0.800	0.500	6.100	4.100	2.250	2.750	ตามไฟล์แบบ
W18	หน้าต่าง	WL01	0.500	1.500	0.501	9.999	0.750	2.250	ตามไฟล์แบบ

ข้อควรใช้ประกอบการวางแผน

1. ขนาดช่องเปิดเป็น nominal ตามไฟล์ ยังไม่มีค่าเพื่อช่องก้อและวงกบที่อนุบัติ
2. ขอบล่าง / หัวช่อง อ้างอิงพื้นผนังในโมเดล ไม่ใช่ระดับพื้นสำเร็จที่ยื่นยื่นหน้างาน
3. D09 เกินปลายผนัง 0.010 ม. และ Zone 8 รูปไม่สมบูรณ์ ควรตรวจแก้ก่อนสั่งผลิตหรือตีราคาขั้นสุดท้าย